




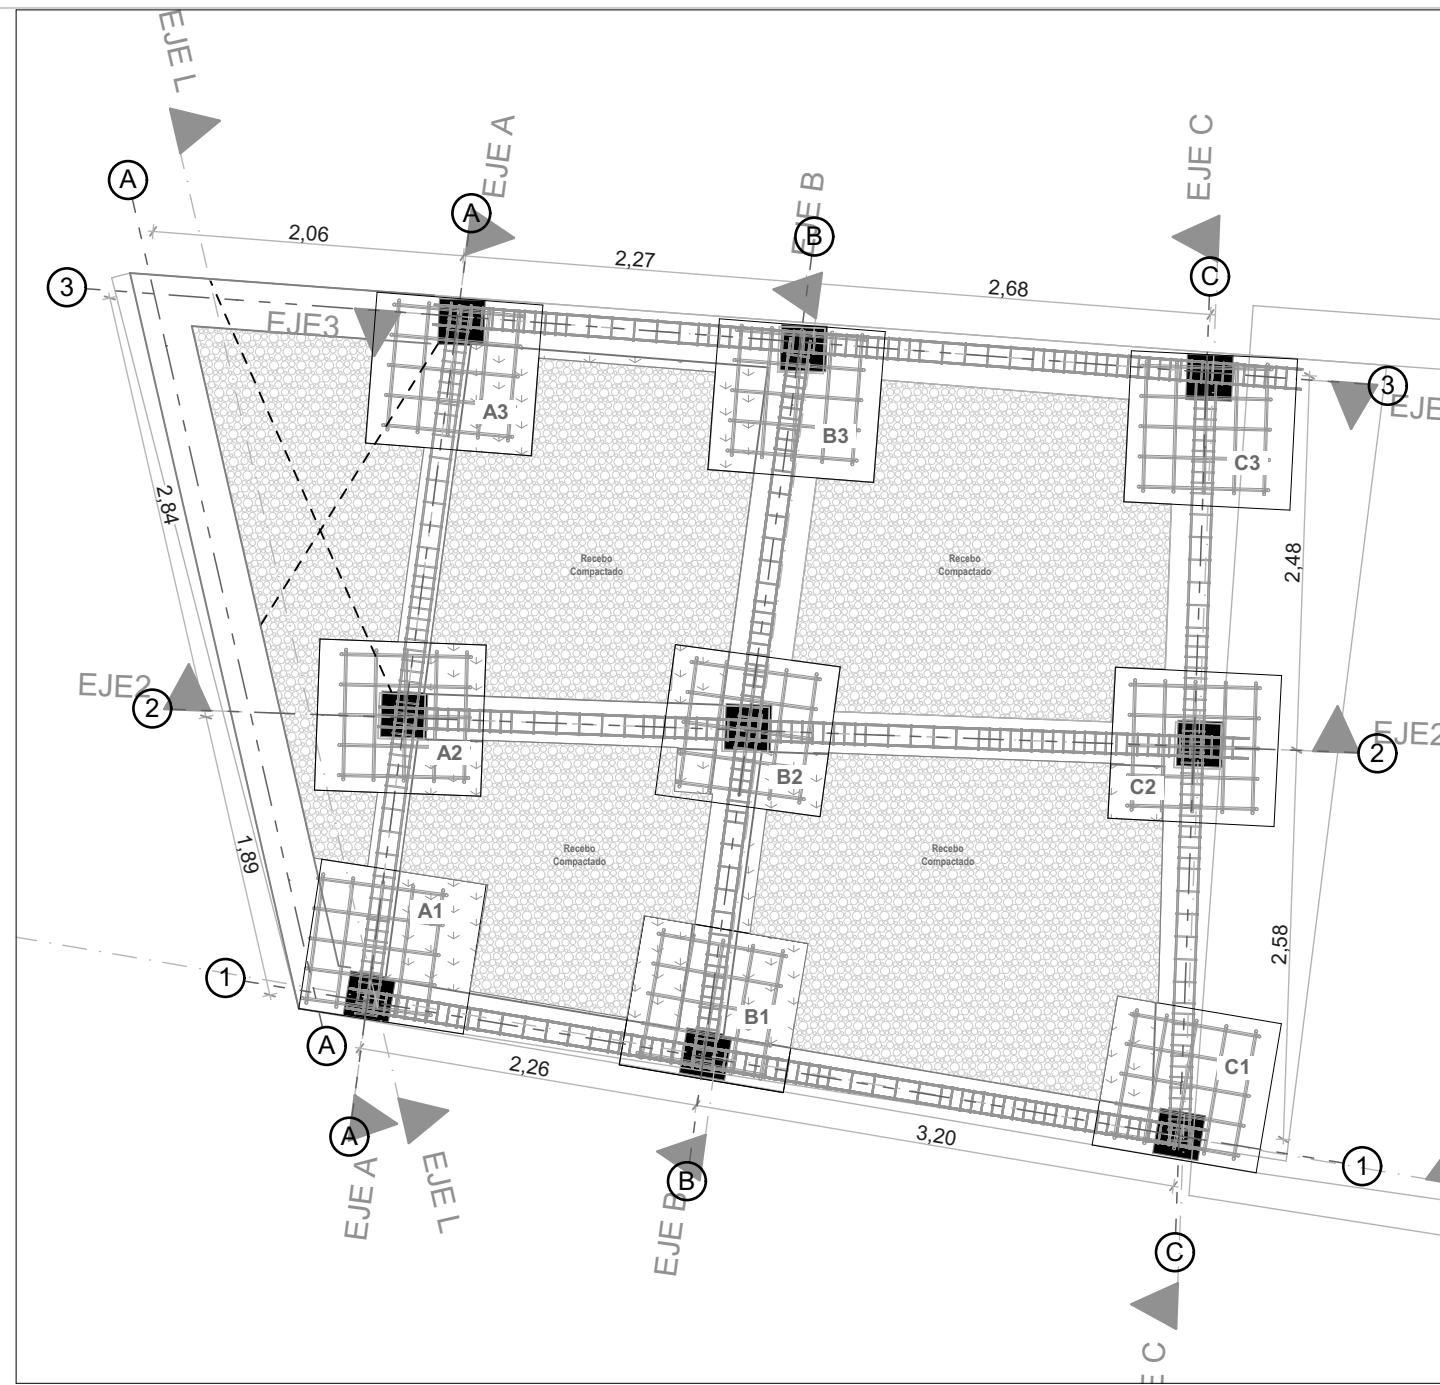




Planta de Cimentación +0.00
Esc 1: 50

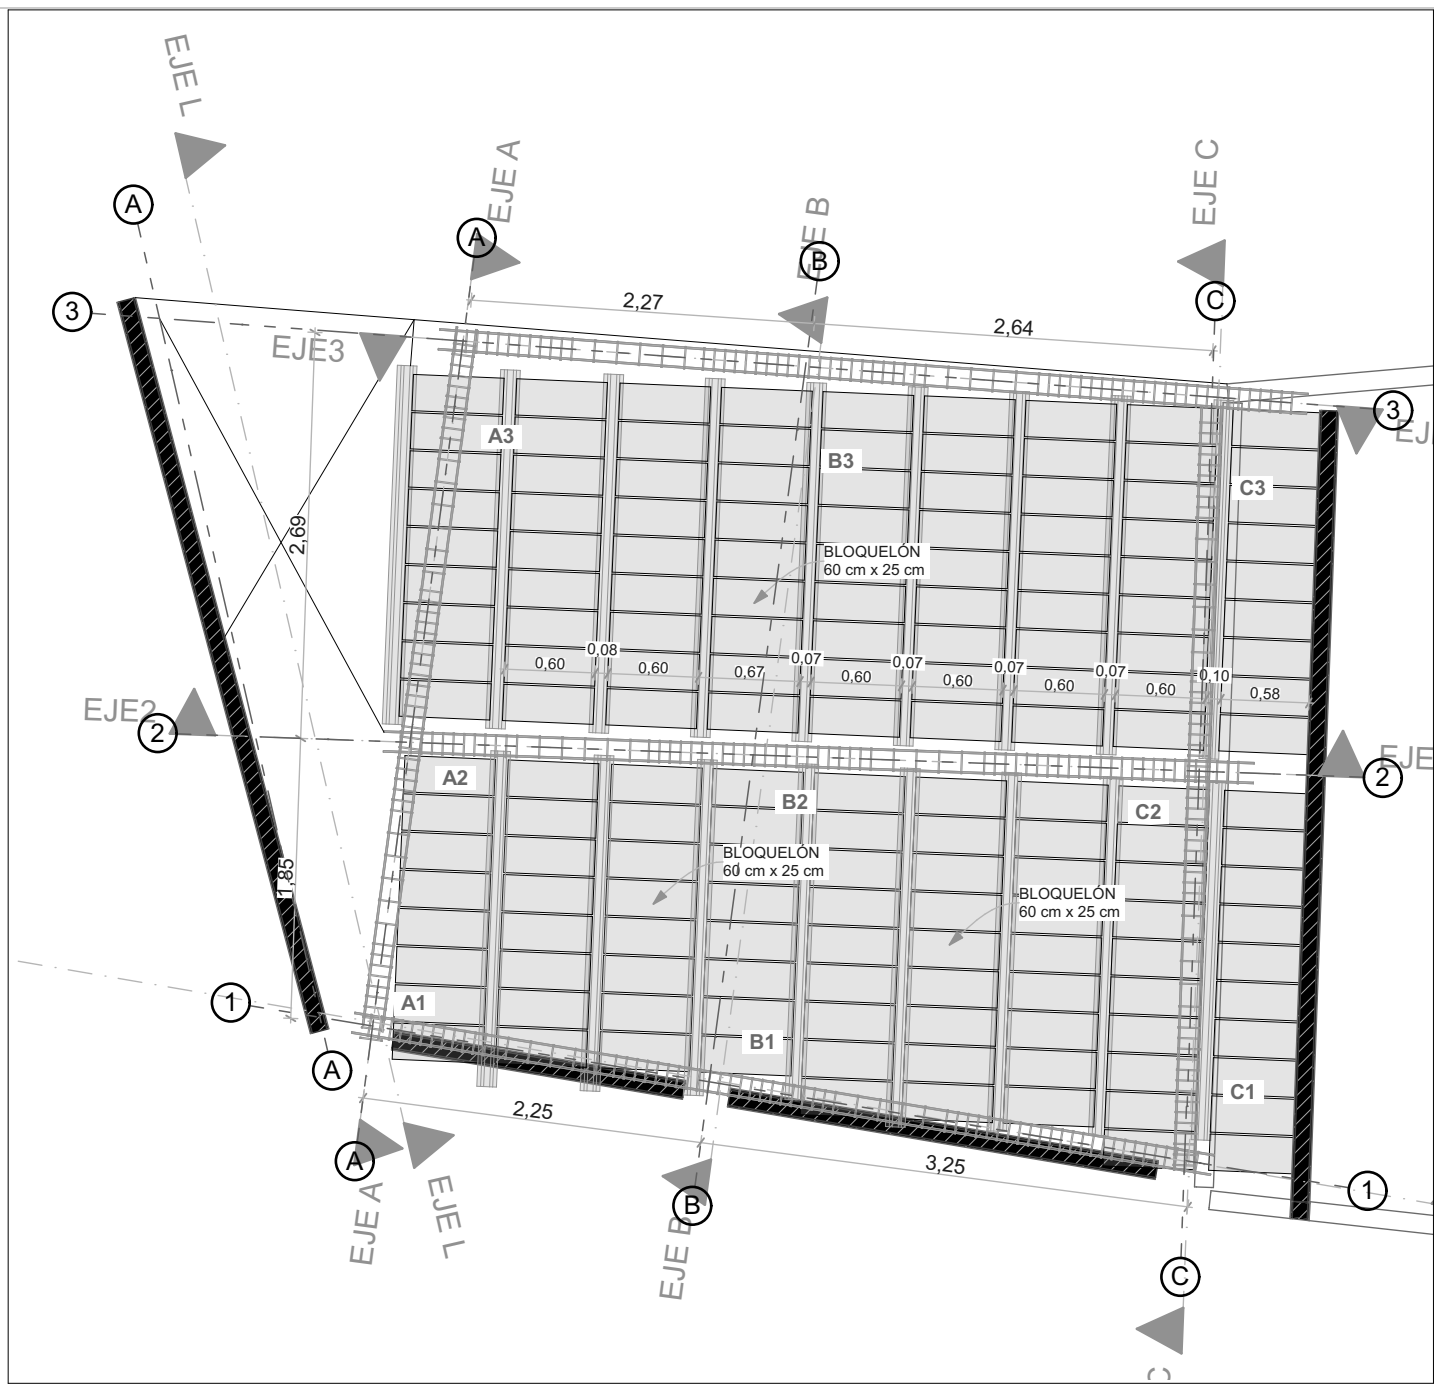


Planta tipo de Entrepiso +2.50 /+5.00
Esc 1: 50

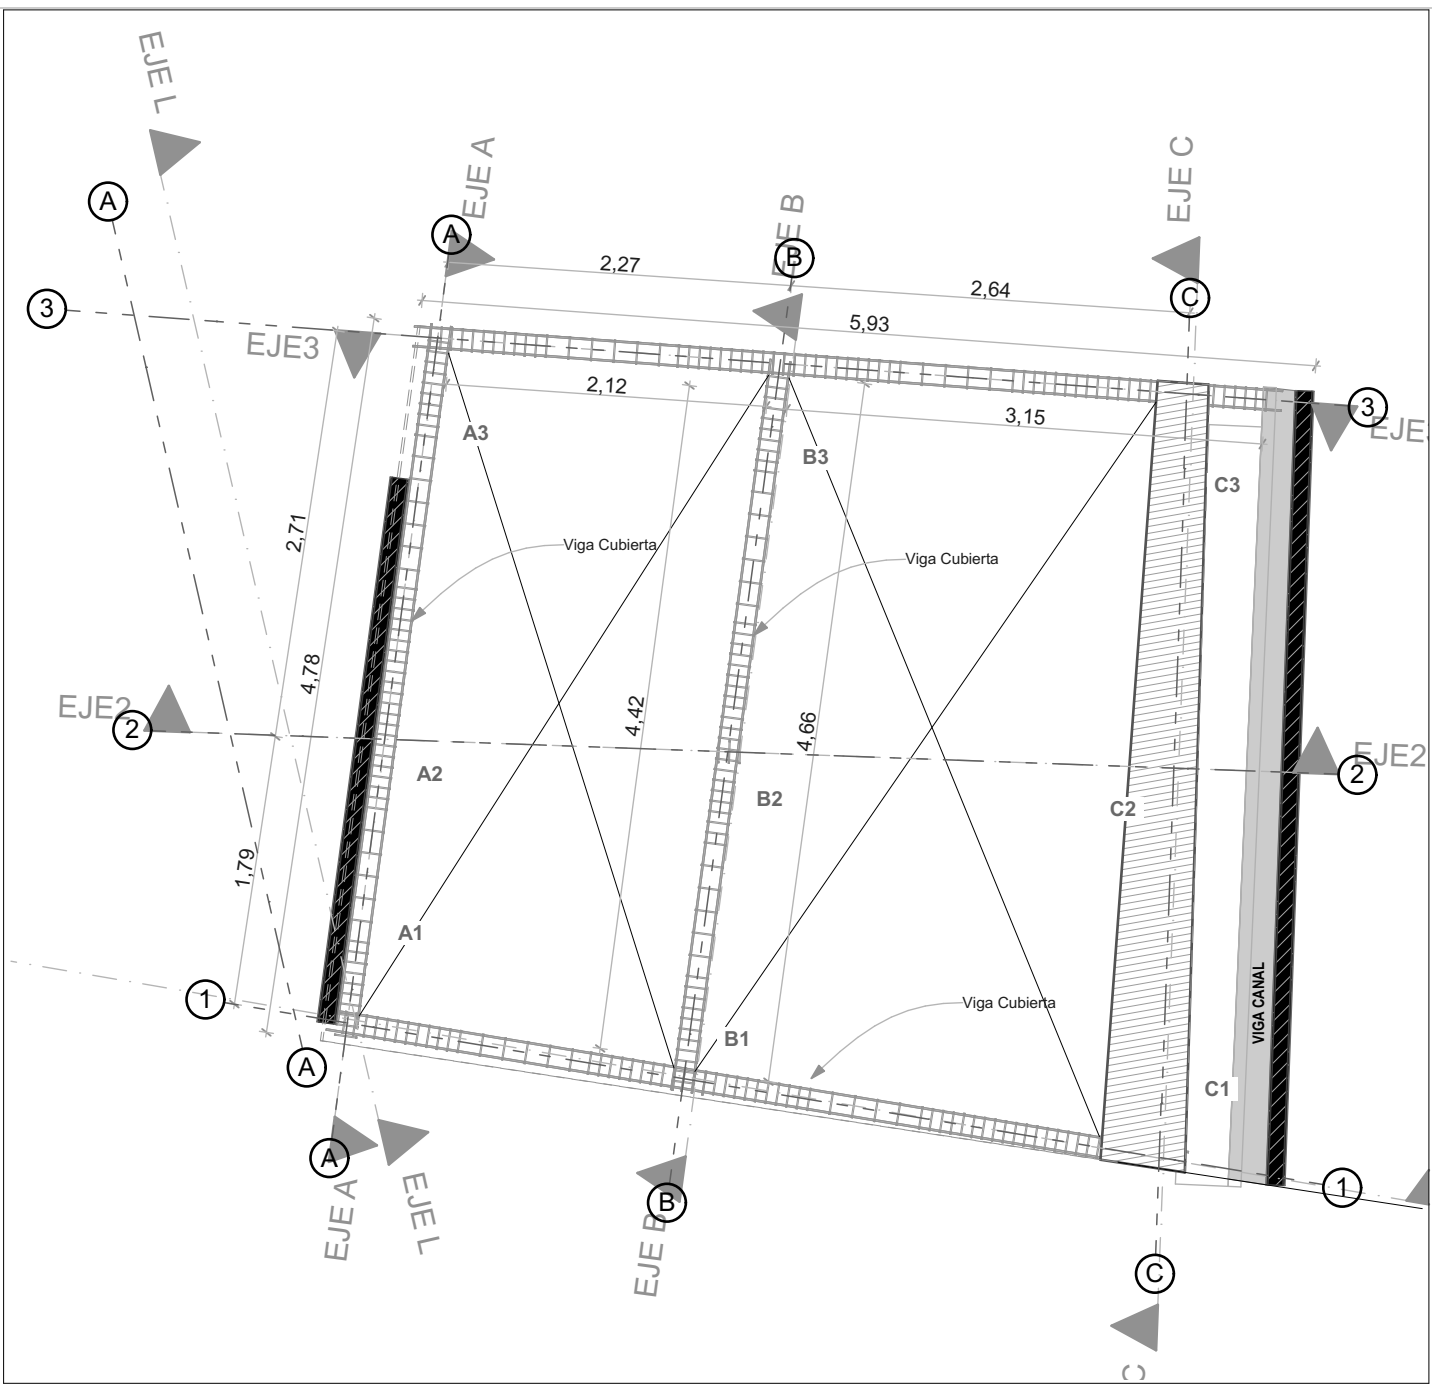


Planta de Cubierta +7.50
Esc 1: 50

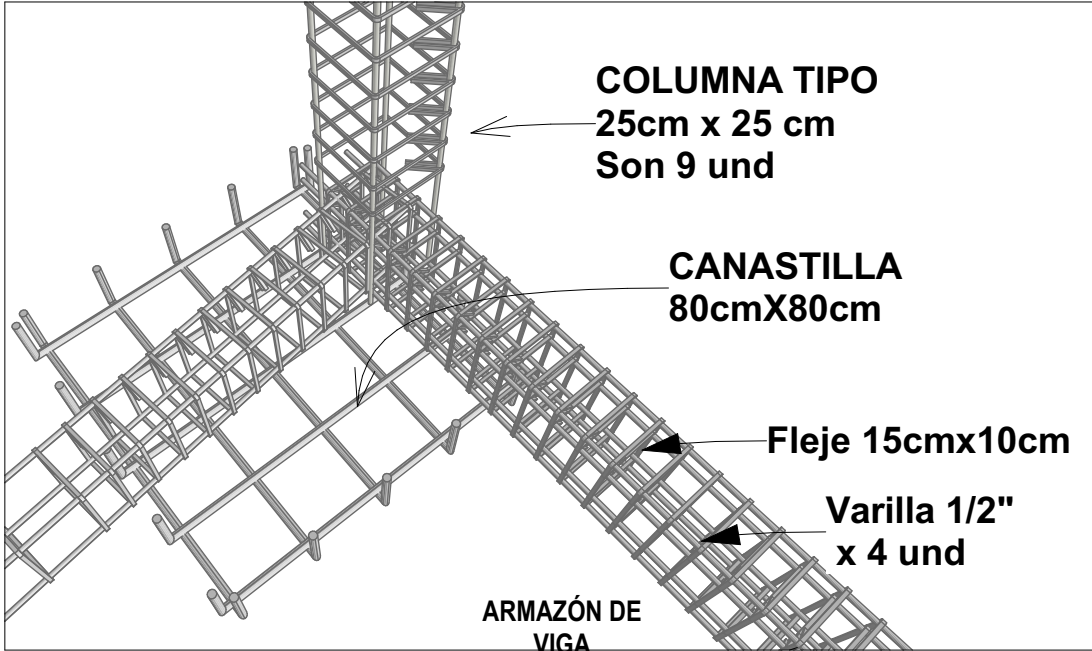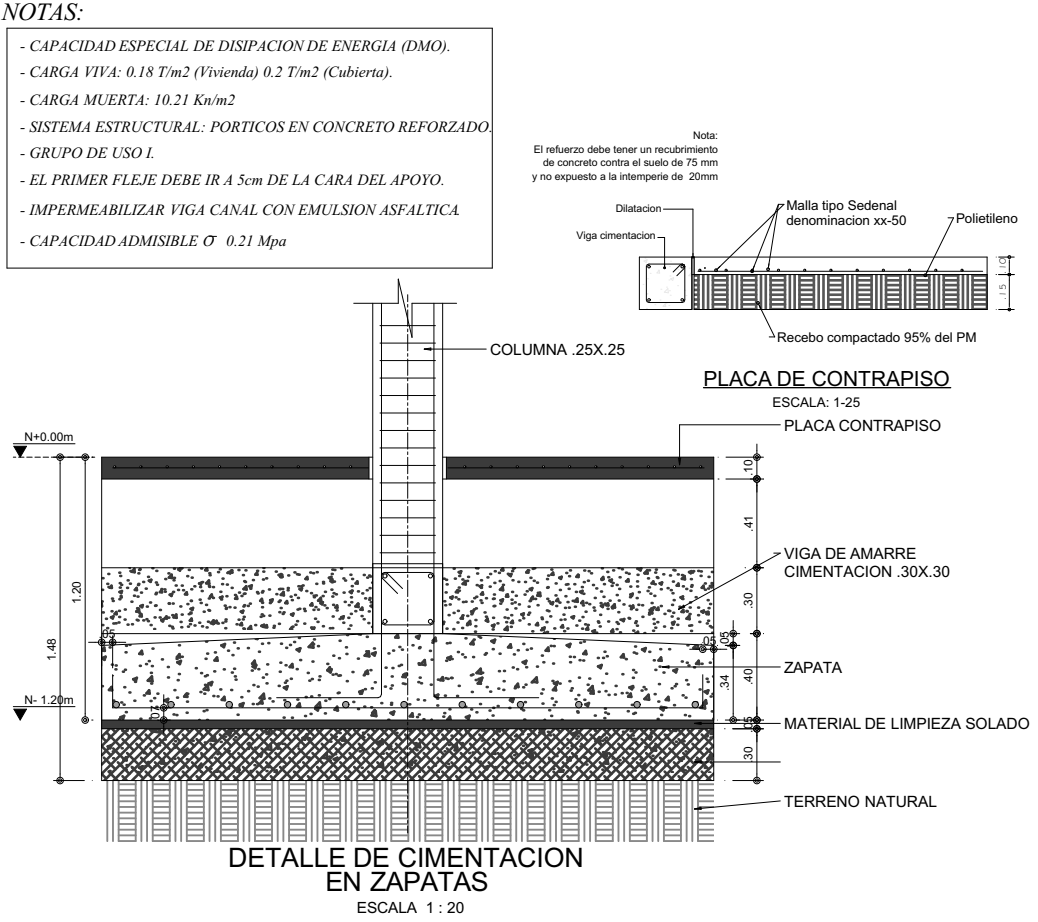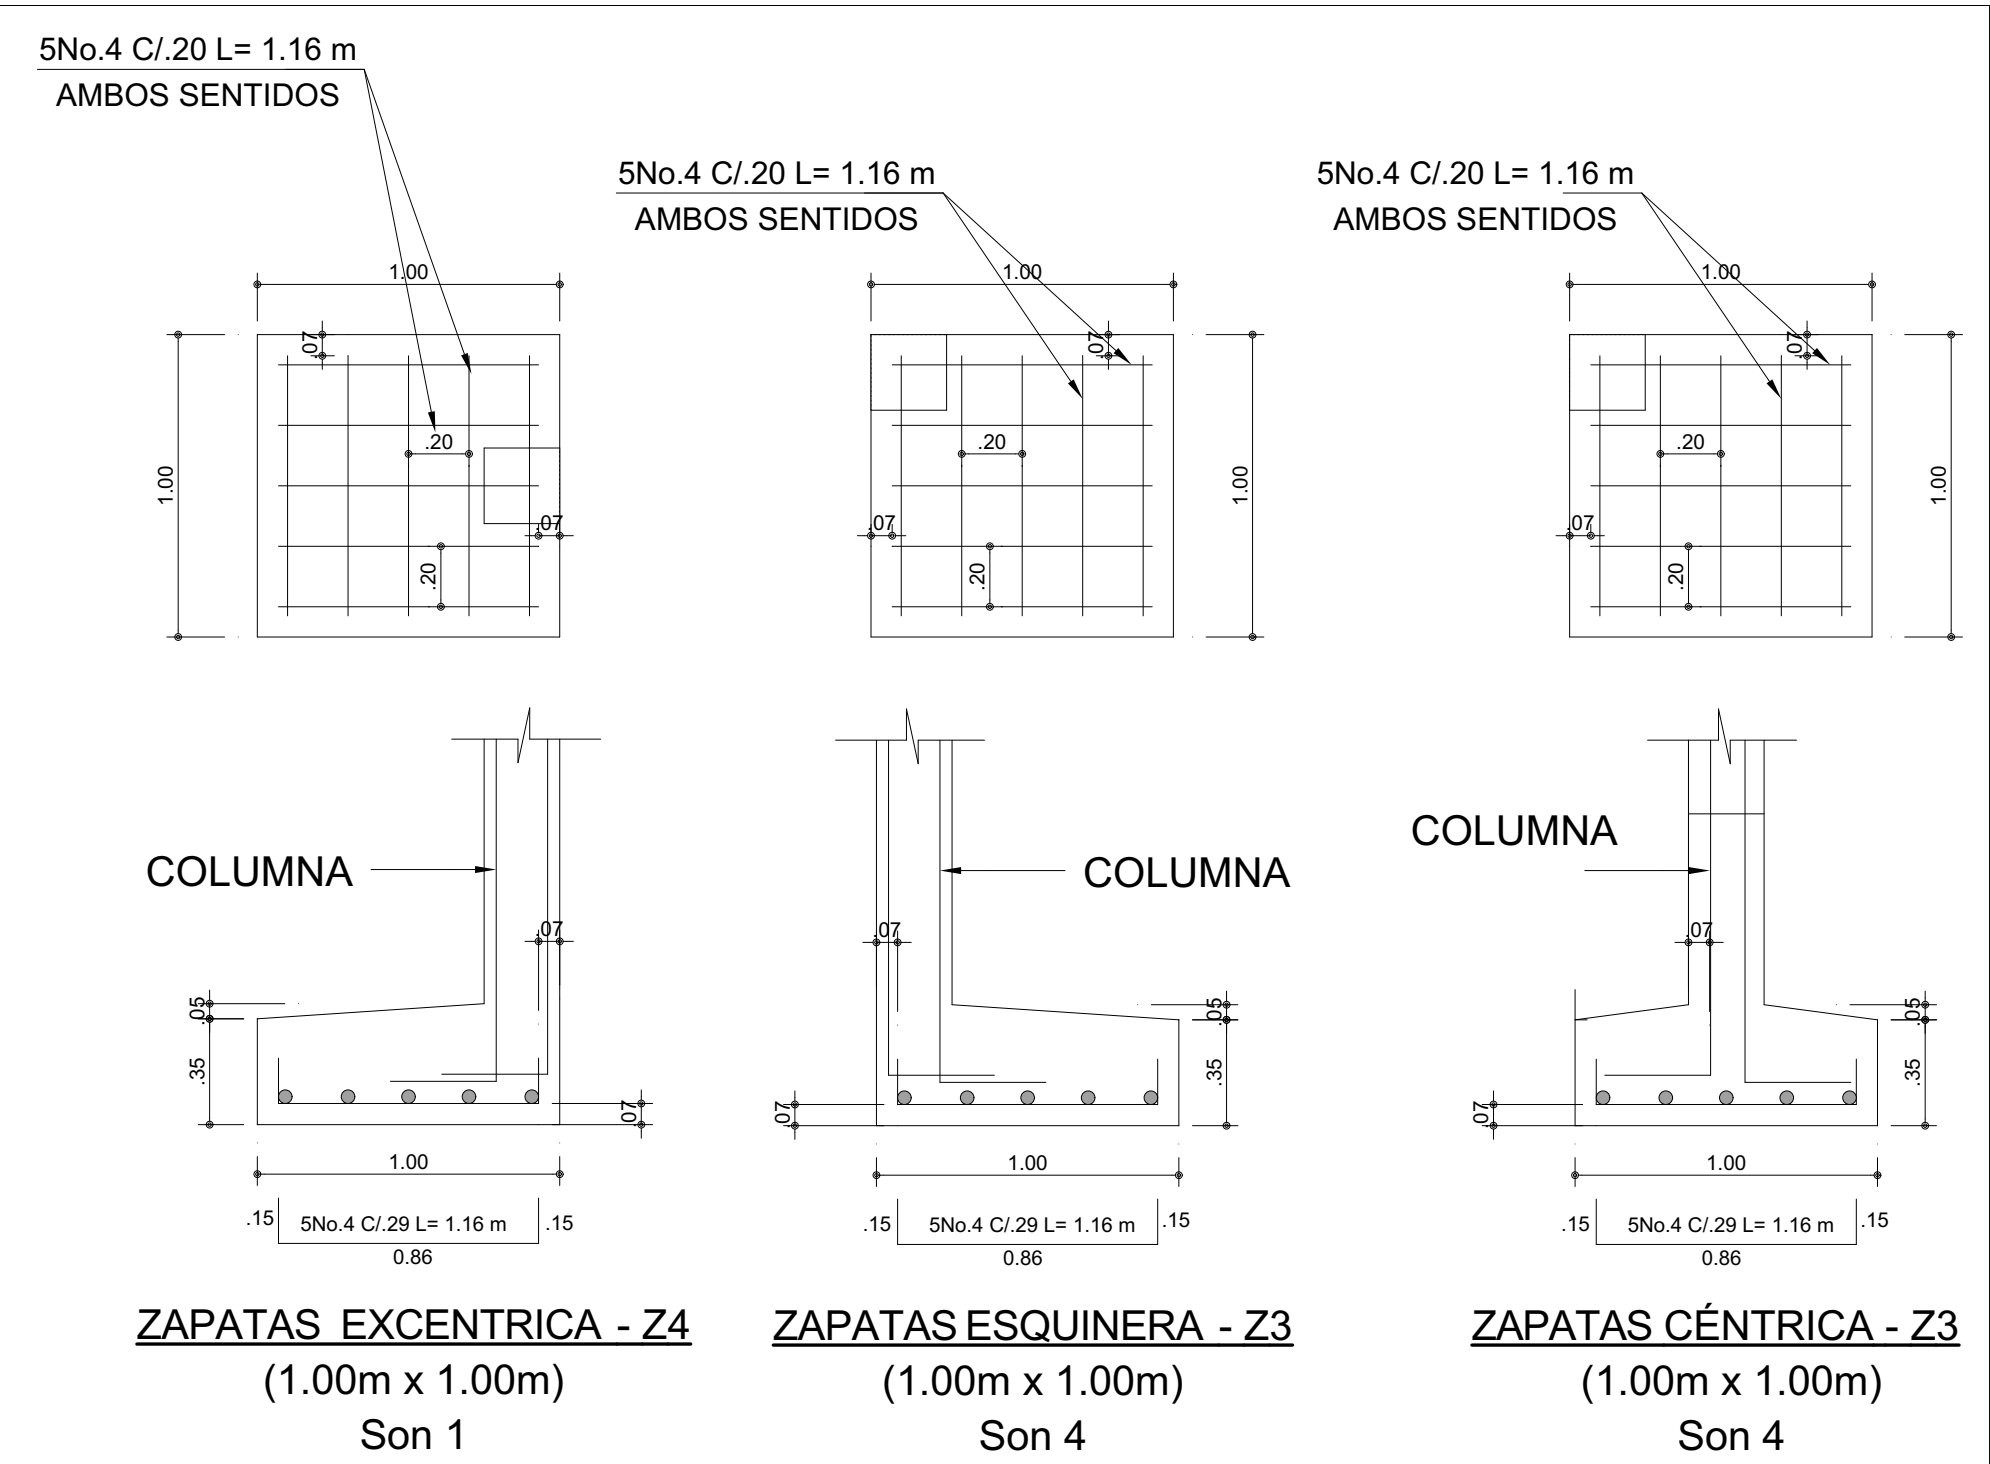

ARMAZÓN DE ZAPATA
VISTA 3D

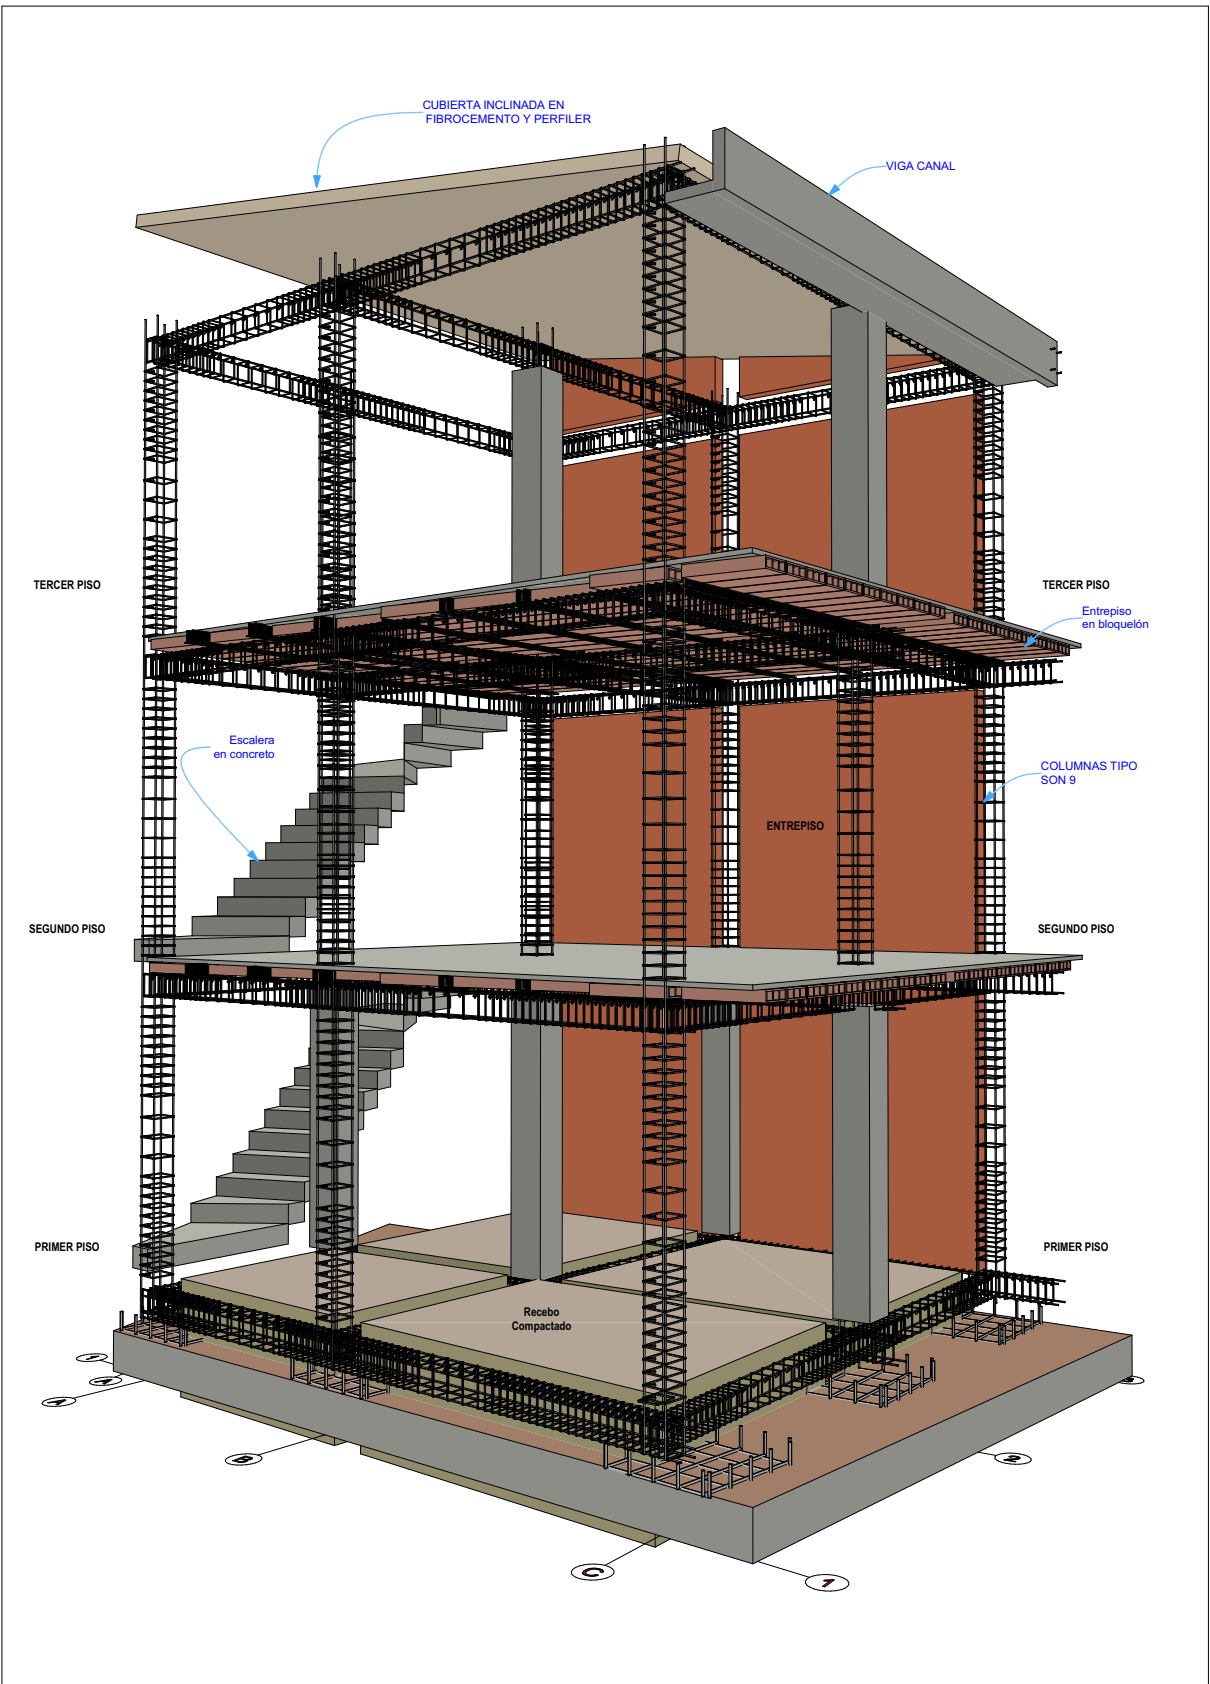

Vista del Proyecto
Axonometría

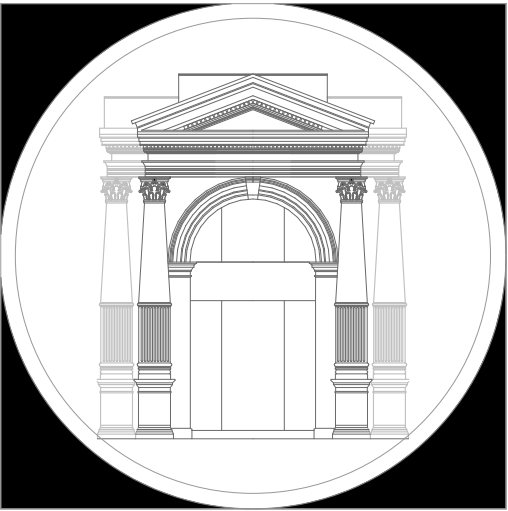

Unifamiliar
"San Esteban"

Localización:
Carrera 16 Calle 22

Arquitecto Proyectista:
Arturo Castro Pacheco
A311162015-1049634950
Arquitecto C.P.N.A.A.
Director de Construcción:

Titular
Nombre: Jeicot E. Rodriguez
Cédula: 6.774.038 de Tunja

Elementos no estructurales:
Nombre: _____
M.P.: _____

Contiene:

Digitó:
GRAFICAD
C.C. 450 AÑOS
LOCAL 118 CRA 9-17-36

Escala:
Segun Indicación
ID:
E1/4
Fecha:
Abril de 2026