
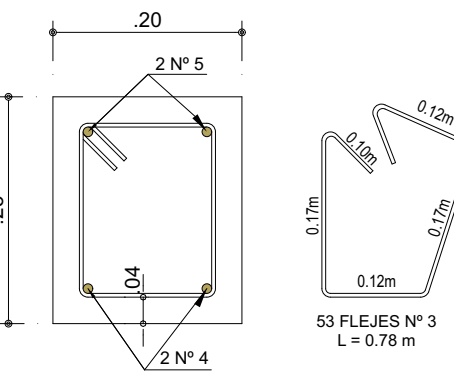
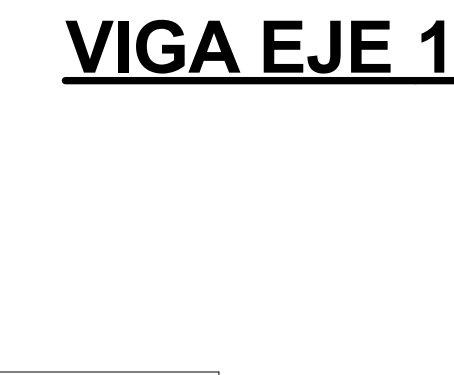


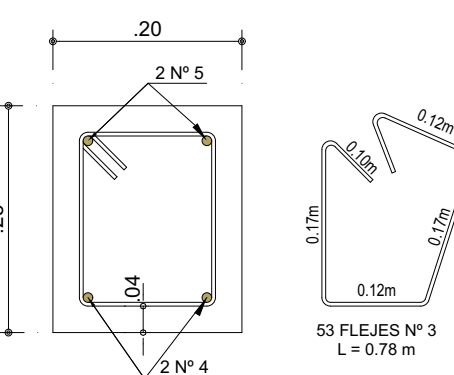

The technical drawing consists of two parts. The left part shows a square cross-section of a column with a side length of 25 units. It features four reinforcement bars: two labeled '2 N° 4' at the top and two labeled '2 N° 5' at the bottom. The right part is a detail of a reinforcement lap, showing two bars overlapping. The lap length is indicated as 'L = 0.88 m'. The drawing also shows the lap length relative to the bar diameter, with dimensions 0.17m, 0.17m, and 0.17m.

25

25

2 N° 4

2 N° 5

0.17m


0.17m

0.17m

66 FLEJES N° 3
L = 0.88 m

COLUMNS

C1=C2=C3=C4=C6=C7=C8=C9



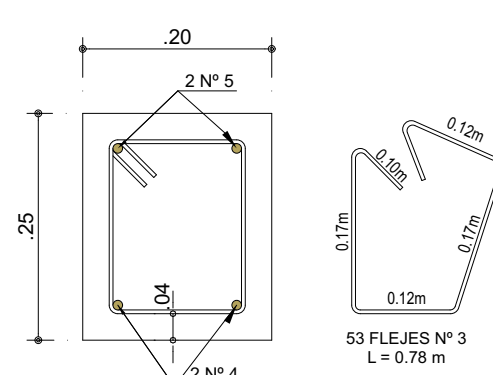


NOTAS:

-

ESPECIFICACIONES DE MATERIALES

- Concretos Prefabricados en Planta de:
 $f'c=4.000 \text{ psi (24.5 Mpa)}$ Columnas y cimientos
 $f'c=3.000 \text{ psi (21 Mpa)}$ Vigas y Otros
 - Acero de refuerzo:
 $f_y=60.000 \text{ psi (420 Mpa)}$
 Factor importancia 1
 calidad de las unidad de mamposteria = 17 Mpa

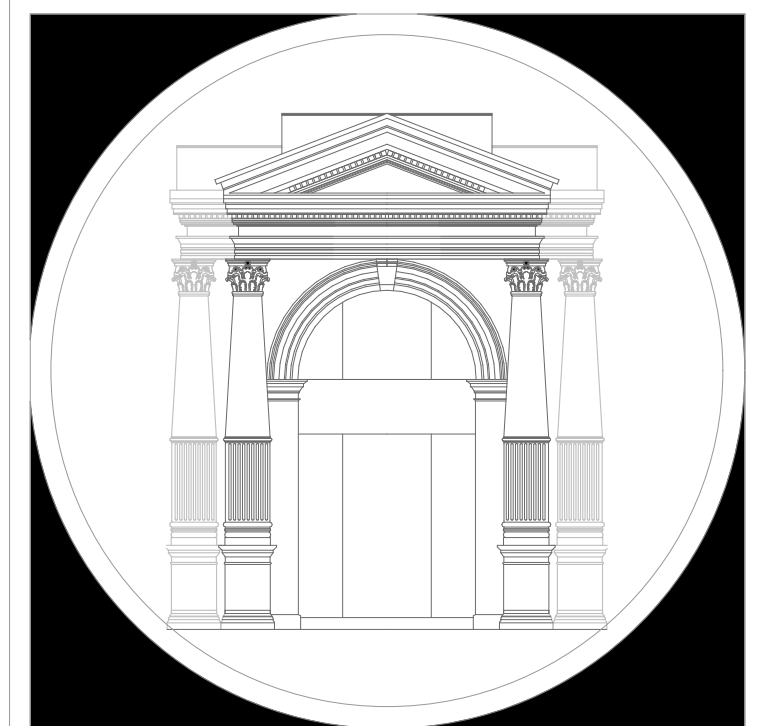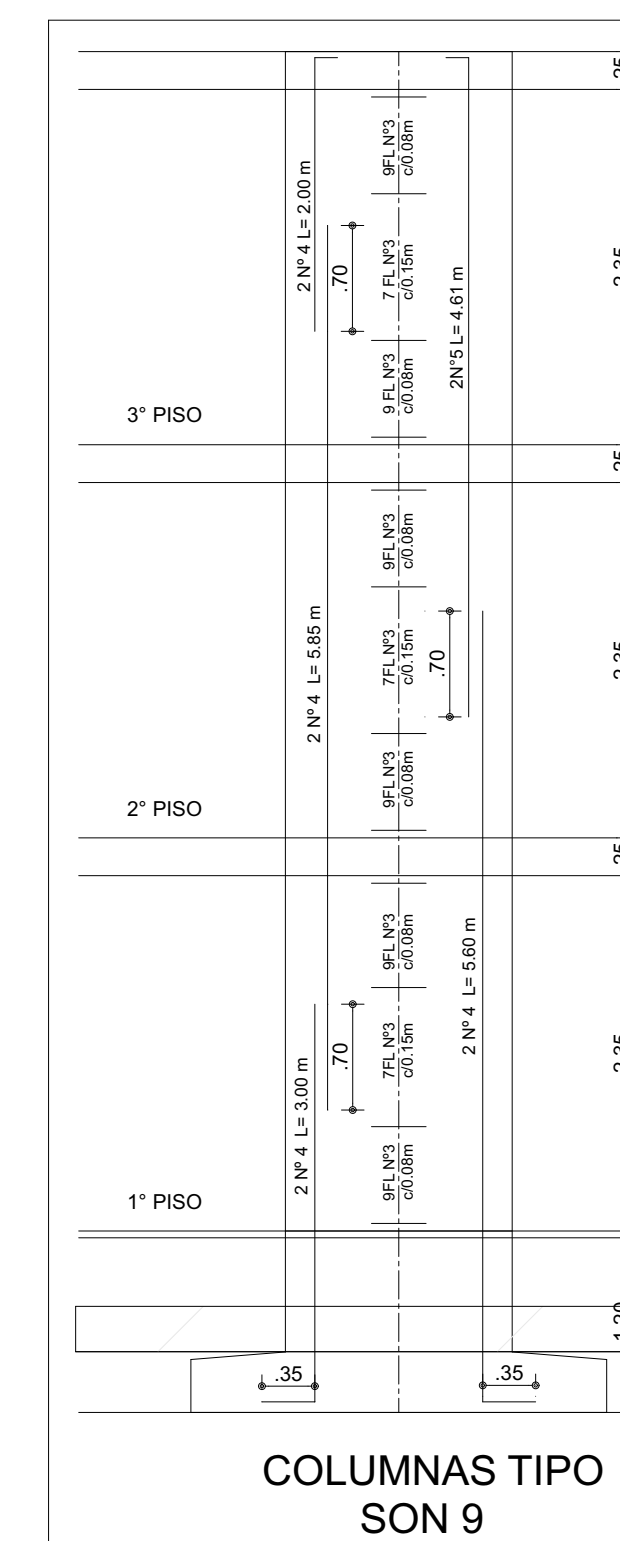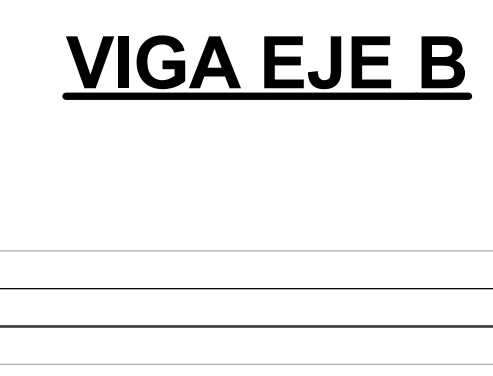

Localización:

Carrera 16 Calle 22

Arquitecto Proyectista:

Arturo Castro Pacheco
A311162015-1049634950
Arquitecto C.P.N.A.A.

Director de Construcción:

Titular

Nombre: Jeicot E. Rodriguez
Cédula: 6.771.038 de Tunja

Elementos no estructurales:

Nombre: _____
M.P.: _____

Contiene:

VIGA A,B,C.1,2 Y 3
DETALLE DE COLUMNA
ALZADO DE COLUMNA
DETALLE DE CORTE DE VIGA

Digitó:

GRAFICA
C.C. 450 AÑOS
LOCAL 118 CRA 9-17-36

Escala:
Segun Indicación

Fecha: Abril de 2026

ID:

E2/4