


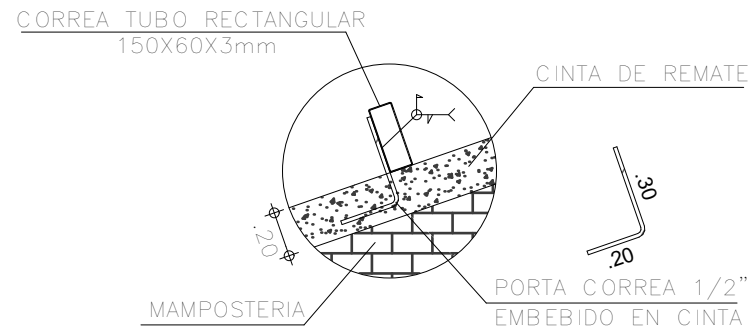


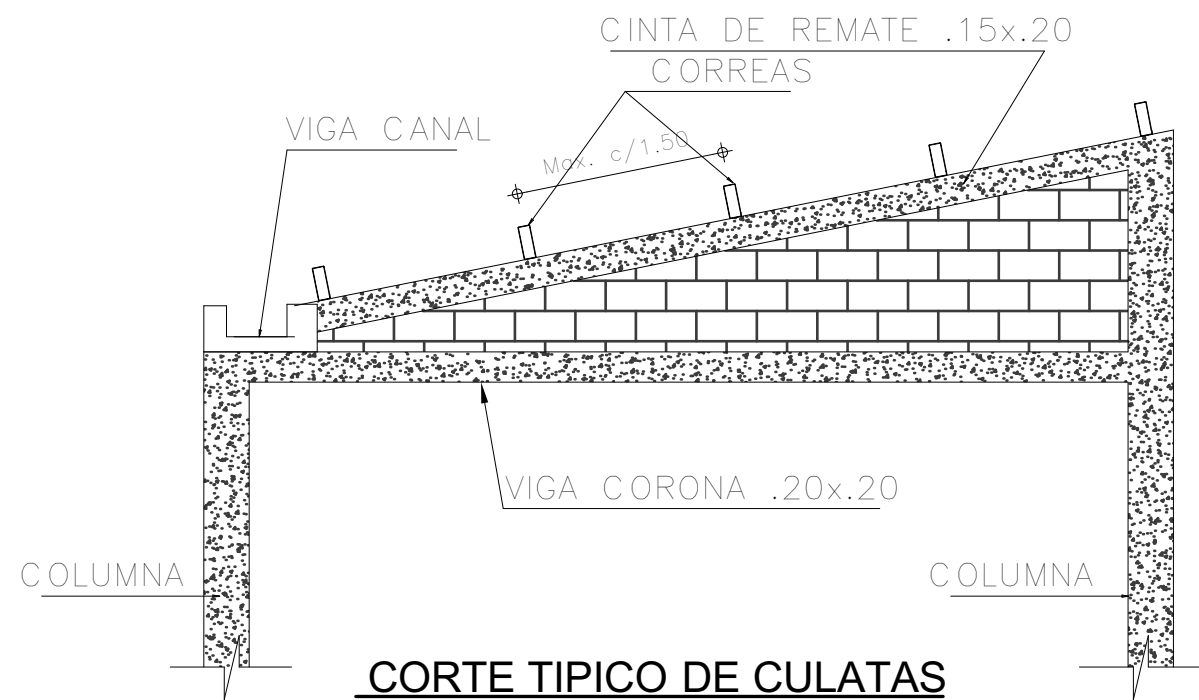

DETALLE DE CORREA
Esc. 1 : 2 5

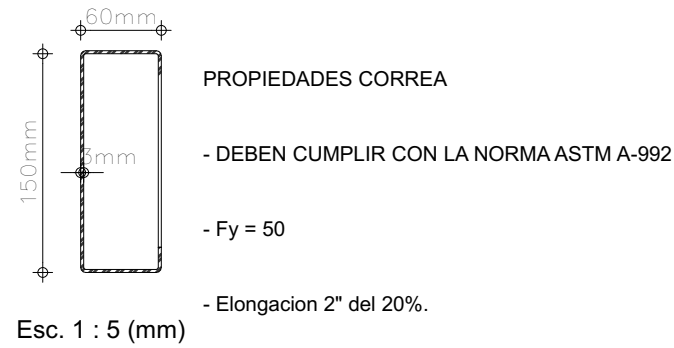


CORTE TIPOICO DE CULATAS
Esc. 1 : 5 0

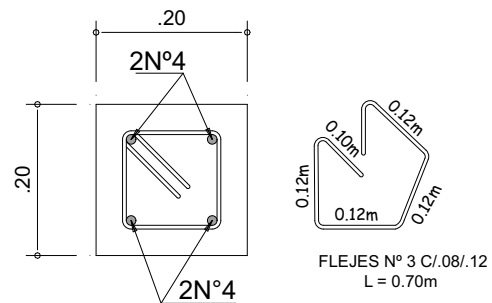


DETALLE VIGA CUBIERTA
(VCU-20x20)

ESCALA: 1-10

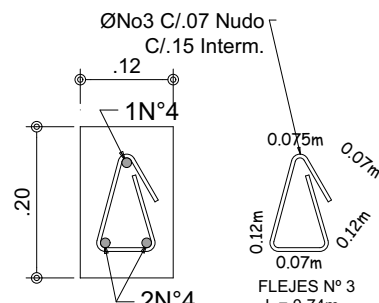


DETALLE VIGA CINTA (VC-15x20)


ESCALA: 1-10

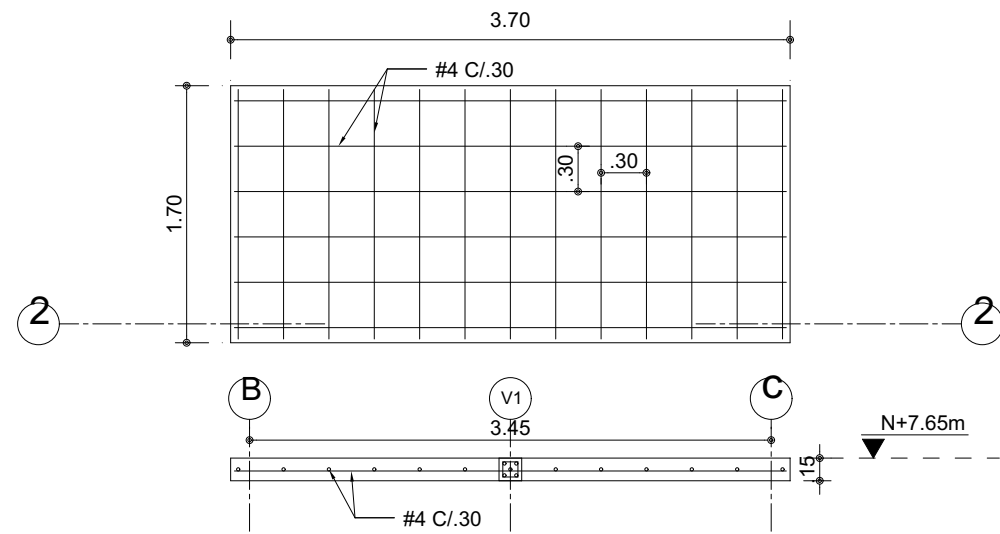


DETALLE PLACA DE TANQUES
ESCALA 1:50

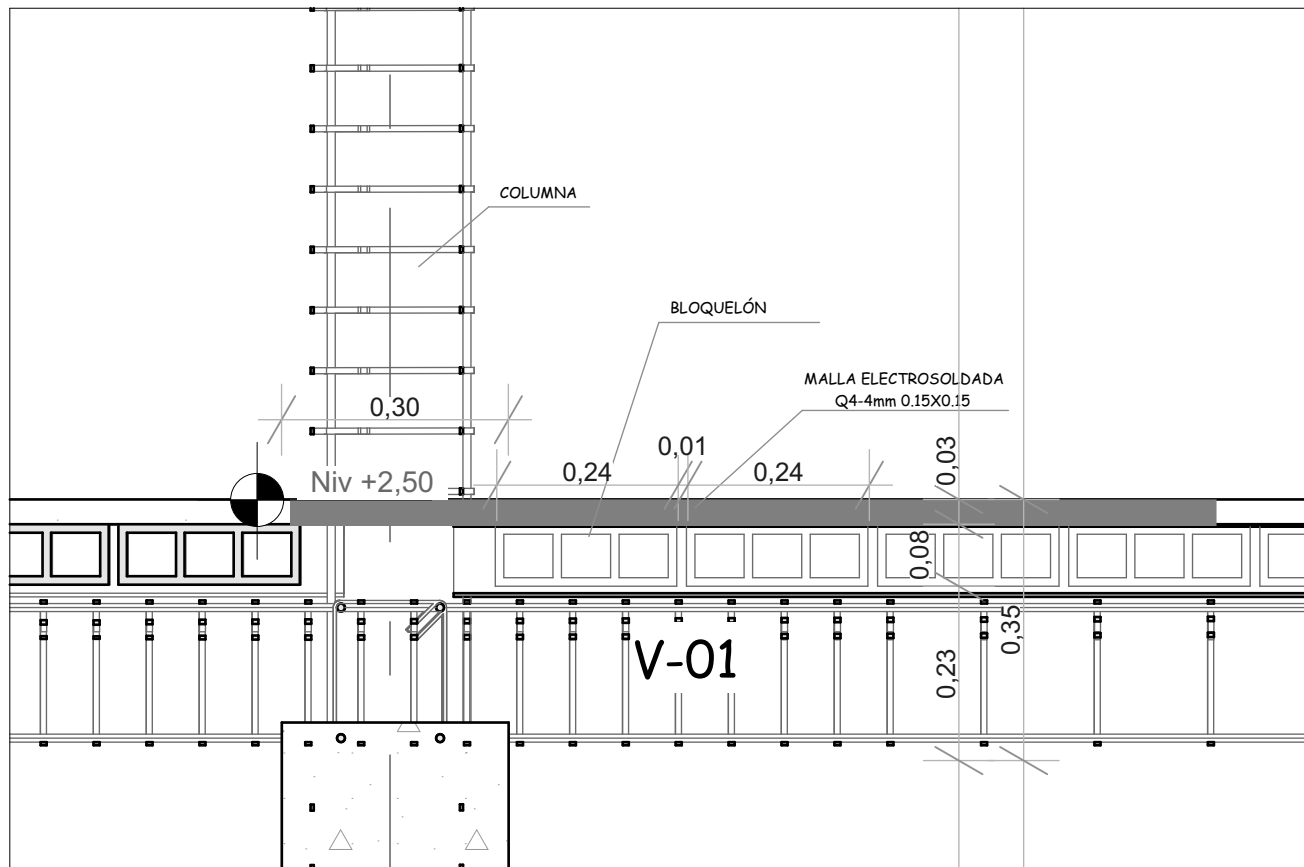

DETALLE DE ENTREPISO
Esc 1: 10

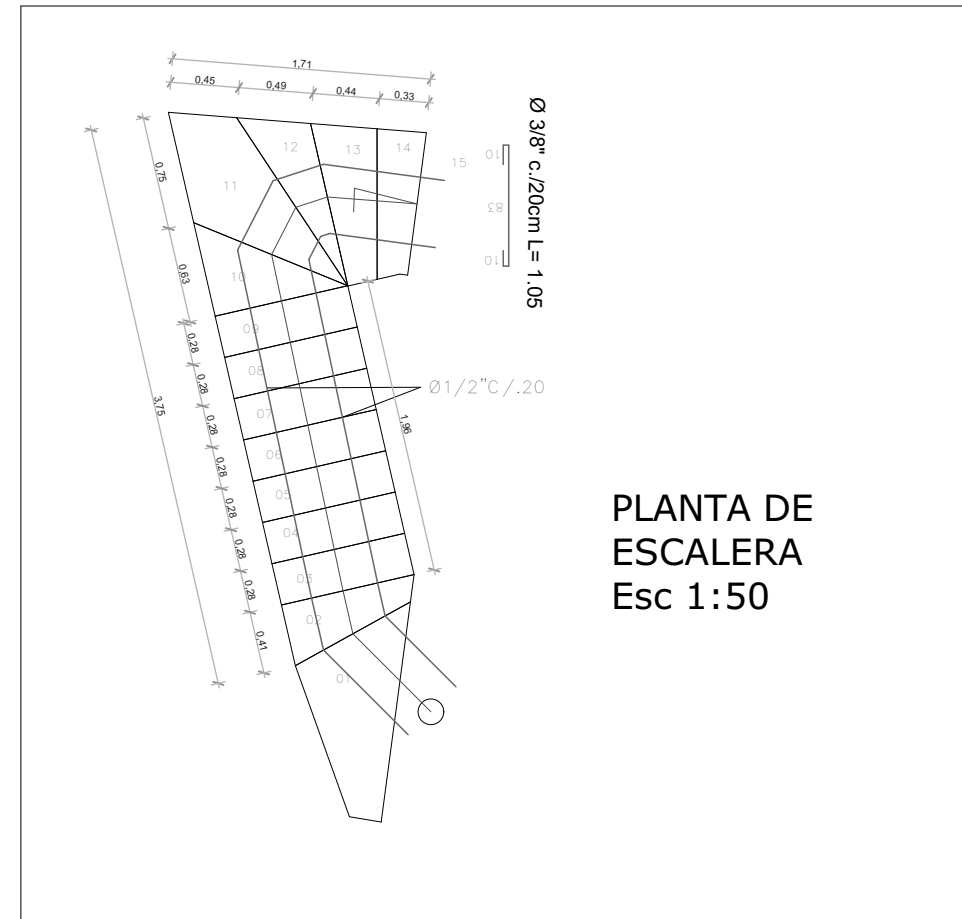

PLANTA DE ESCALERA
Esc 1:50

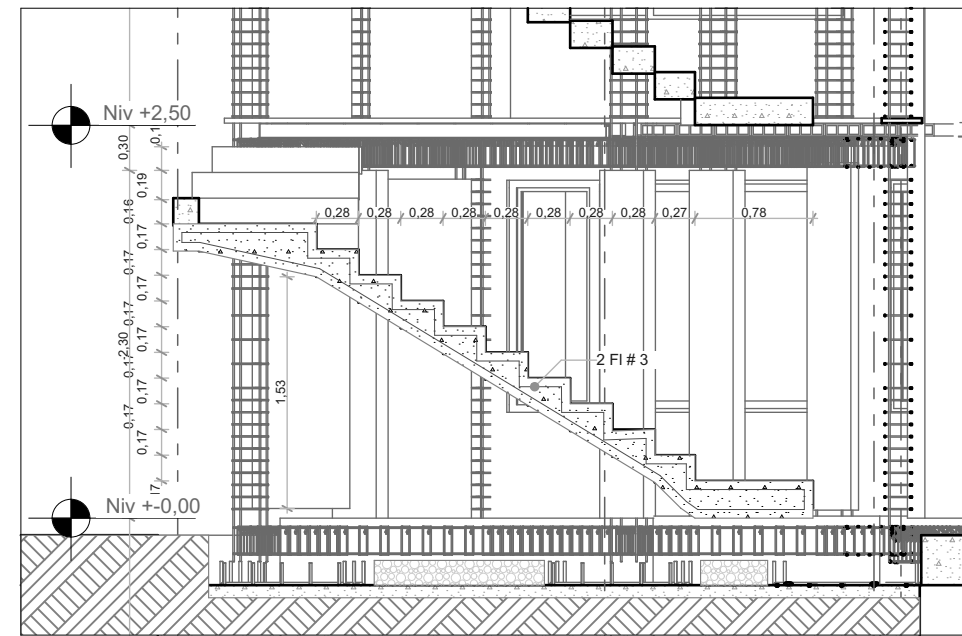

ALZADO DE ESCALERA
Esc 1: 50

NOTAS:

- CAPACIDAD ESPECIAL DE DISIPACION DE ENERGIA (DMO).
- CARGA VIVA: 0.18 T/m2 (Vivienda) 0.2 T/m2 (Cubierta).
- CARGA MUERTA: 10.21 Kn/m2
- SISTEMA ESTRUCTURAL: PORTICOS EN CONCRETO REFORZADO.
- GRUPO DE USO I.
- EL PRIMER FLEJE DEBE IR A 5cm DE LA CARA DEL APOYO.
- IMPERMEABILIZAR VIGA CANAL CON EMULSION ASFALTICA
- CAPACIDAD ADMISIBLE σ 0.21 Mpa

ESPECIFICACIONES DE MATERIALES

- Concretos Prefabricados en Planta de: $f'c=4.000$ psi (24.5 Mpa) Columnas y cimientos $f'c=3.000$ psi (21 Mpa) Vigas y Otros
- Acero de refuerzo: $f_y=60.000$ psi (420 Mpa)
- Factor importancia 1
- calidad de las unidad de mamposteria = 17 Mpa

CUADRO DE TRASLAPOS MINIMOS

Barra	REFUERZO VIGAS		COLUMNAS
	COMPRESION	TRACCION	
#2	0.30	0.40	0.40
#3	0.45	0.60	0.60
#4	0.60	0.70	0.70
#5	0.70	0.90	0.90
#6	0.85	1.00	1.00
#7	1.20	1.60	1.60
#8	1.40	1.80	1.80

Las unidades se encuentran en metros



CUADRO DE GANCHOS

Barra	REFUERZO PRINCIPAL			RESTRIBOS
	90°	180°	135° - 180°	
#2	0.08	0.08	0.08	
#3	0.13	0.13	0.08	
#4	0.20	0.15	0.10	
#5	0.25	0.20	-	
#6	0.30	0.25	-	
#7	0.35	0.30	-	
#8	0.40	0.35	-	

Las unidades se encuentran en metros

DIMENSIONES PARA EL DOBLAMIENTO DE VARILLAS						
DIMENSIONES (en mm) PARA GANCHOS ESTANDAR						
Para el doblamiento de las barras de refuerzo principal						
BARRA No.	GANCHO 90°			GANCHO 180°		
	D	L	C	D	L	C
#4	76.2	190	102	102	222	203
#5	95.4	238	122	122	278	254
#6	114.6	286	153	153	334	306
#7	133.2	333	178	178	388	355
#8	152.4	381	203	203	444	406
#9	229.5	521	258	258	547	488
#10	258.4	586	291	291	616	549
#11	285.4	649	322	322	683	609
#14	430.0	915	430	430	887	774
#18	573.0	1219	573	573	1183	1030

Planta de Cubierta
Esc 1: 50

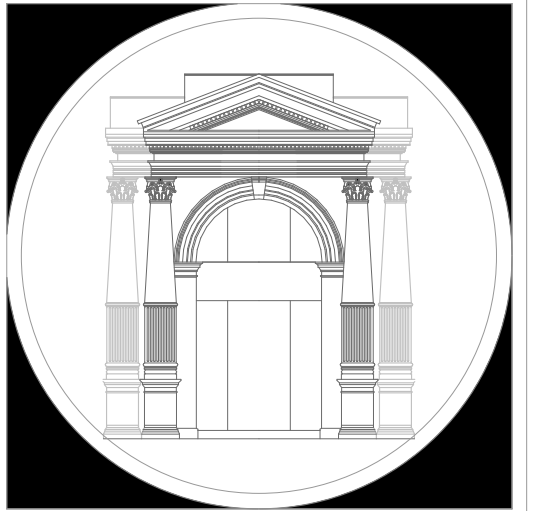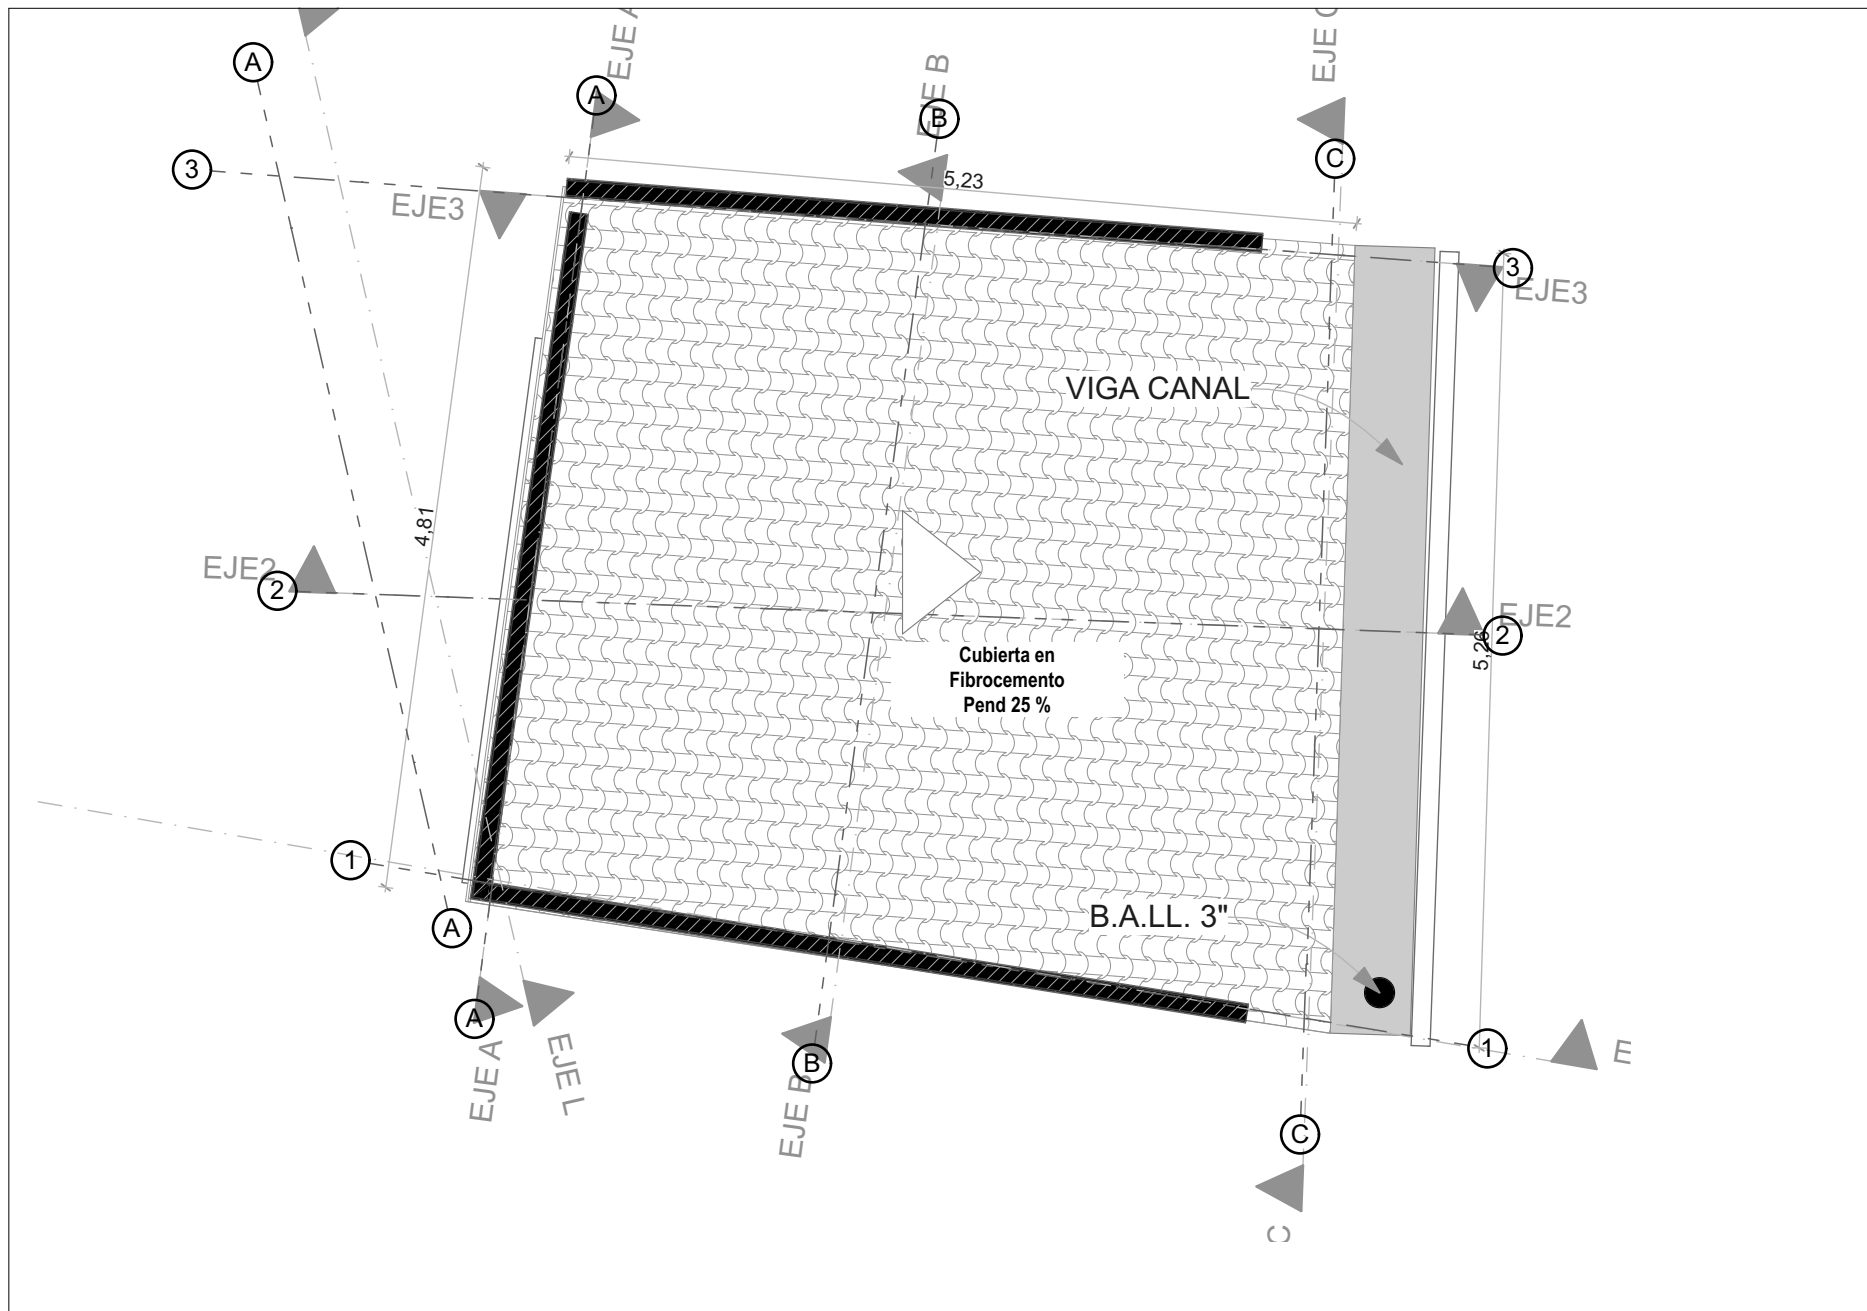

Unifamiliar "San Esteban"

Localización:

Carrera 16 Calle 22

Arquitecto Proyectista:

Arturo Castro Pacheco
A311162015-1049634950
Arquitecto C.P.N.A.A.

Director de Construcción:

Titular

Nombre: Jeicot E. Rodriguez
Cédula: 6.774.038 de Tunja

Elementos no estructurales:

Nombre: _____
M.P.: _____

Contiene:

PLANTA DE ESCALERA
ALZADO DE ESCALERA
DETALLE DE ENTREPISO
CULATA
DETALLE MATERIALES

Digitó:

GRAPHICAD
C.C. 450 AÑOS
LOCAL 118 CRA 9-17-36

Escala:
Segun Indicación

Fecha:
Abril de 2026

ID:

E3/4