




DETALLES DE ELEMENTOS NO ESTRUCTURALES

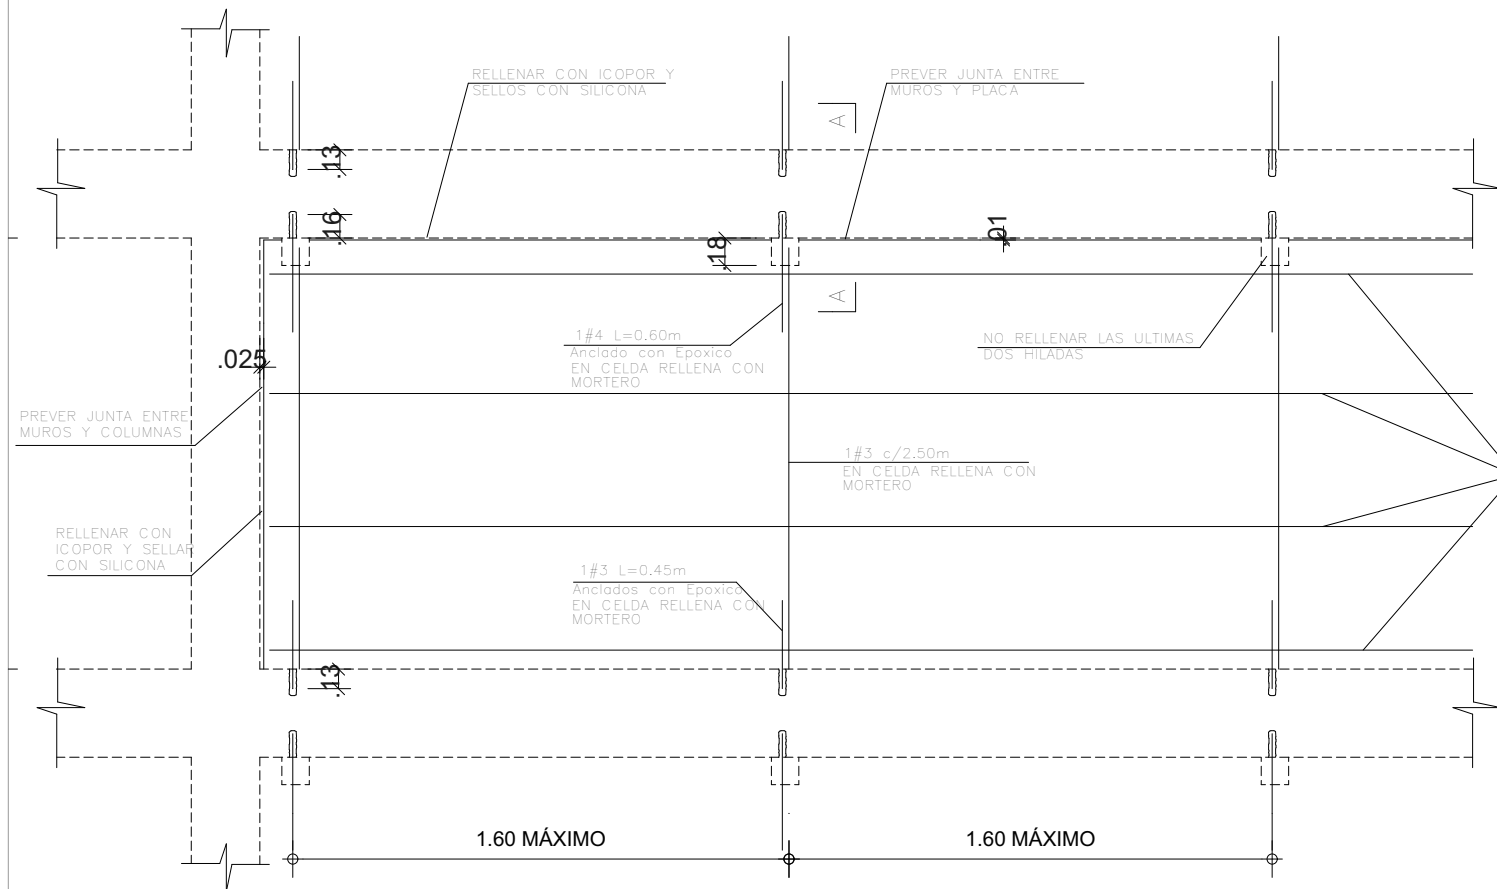


VISTA FRONTAL
REFUERZO TÍPICO DE MUROS DE FACHADA
DE ALTURA TOTAL EN LADRILLO TOLETE $e = 0.15 \text{ m}$
ESC 1:25

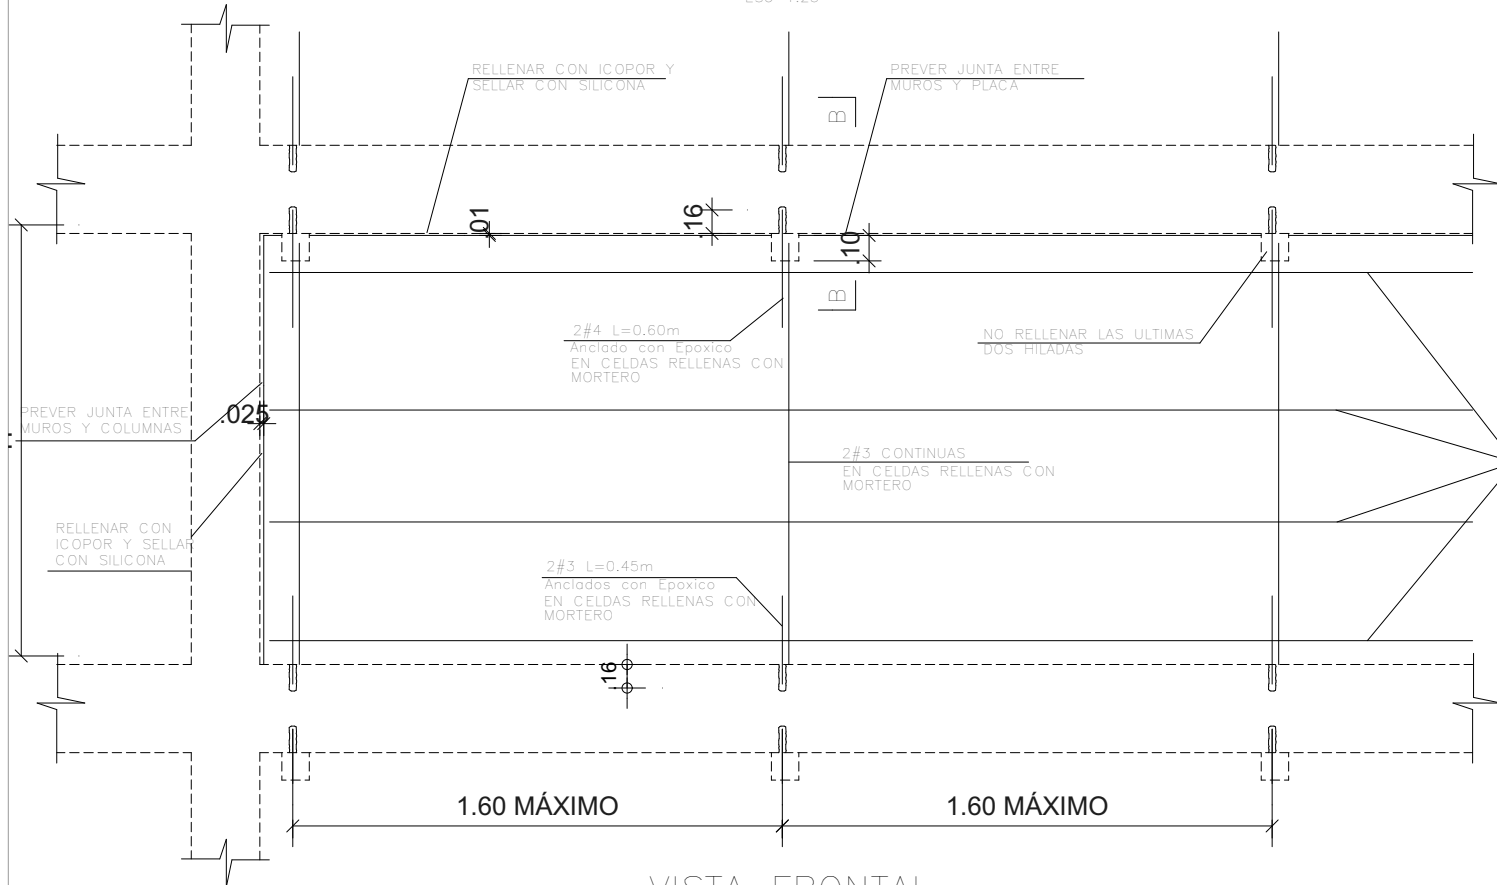


VISTA FRONTAL
REFUERZO TÍPICO DE MUROS DE FACHADA
DE ALTURA TOTAL EN LADRILLO TOLETE $e = 0.25 \text{ m}$
ESC 1:25

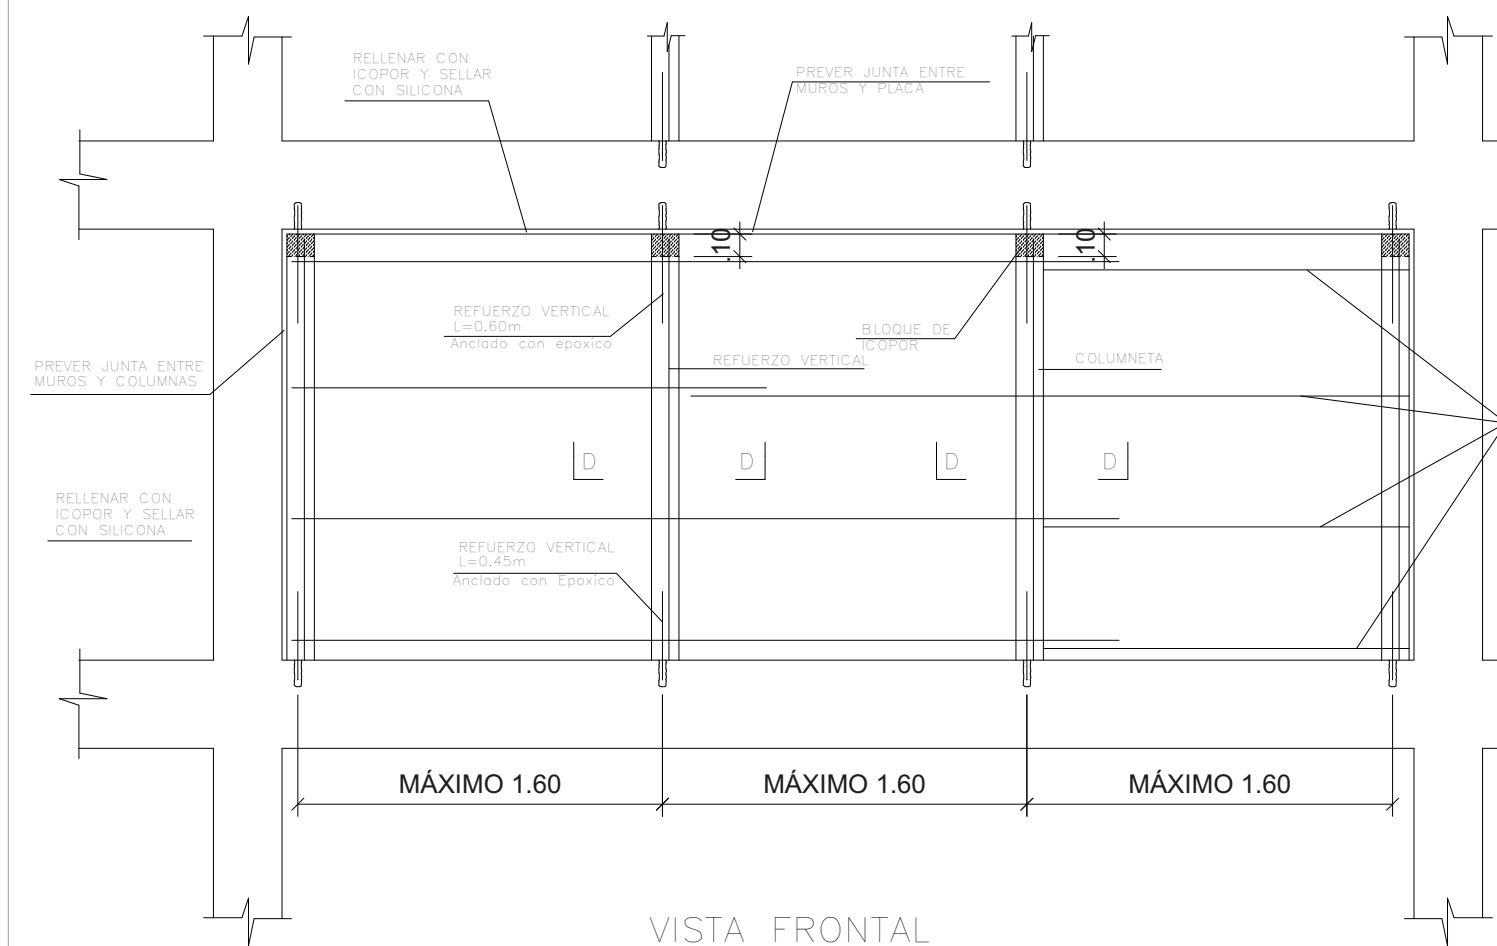


VISTA FRONTAL
REFUERZO TÍPICO DE MUROS DIVISORIOS
DE ALTURA TOTAL EN BLOQUE DE PERFORACIÓN HORIZONTAL
ESC 1:25

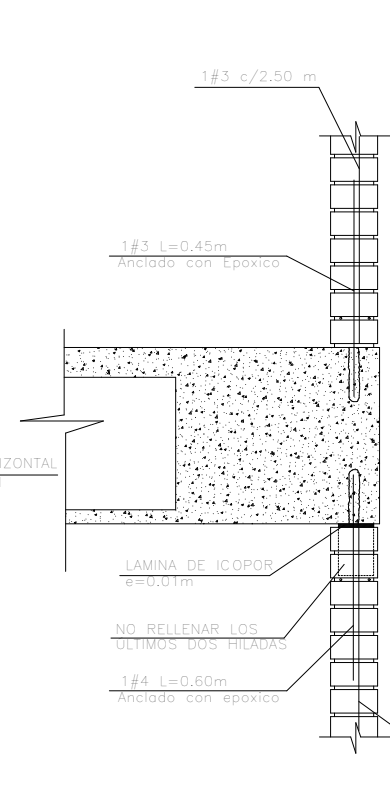


SECCIÓN A-A
ESC 1:12.5

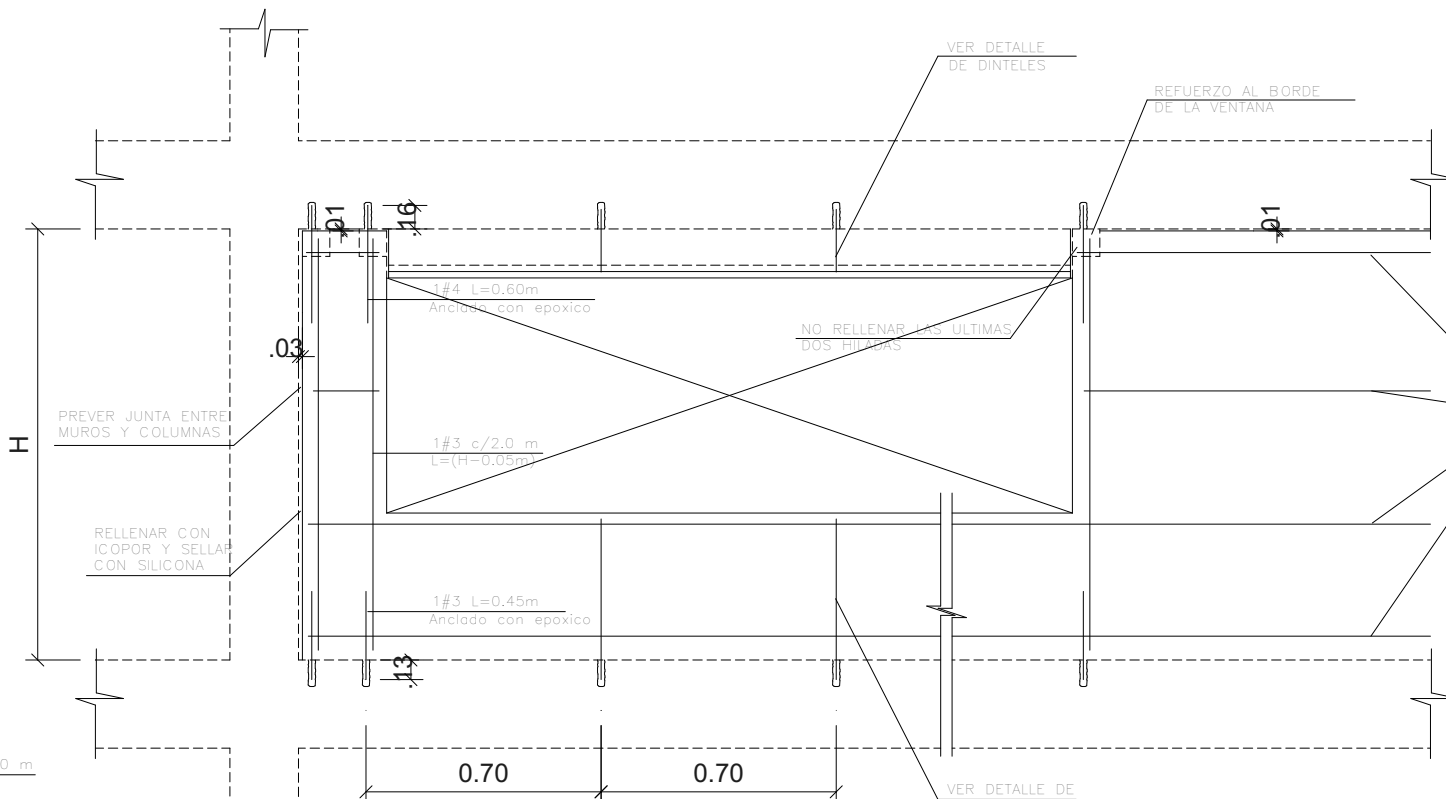


VISTA FRONTAL
REFUERZO TÍPICO DE MUROS EN LADRILLO TOLETE $e=0.15 \text{ m}$ CON ABERTURA
ESC 1:25

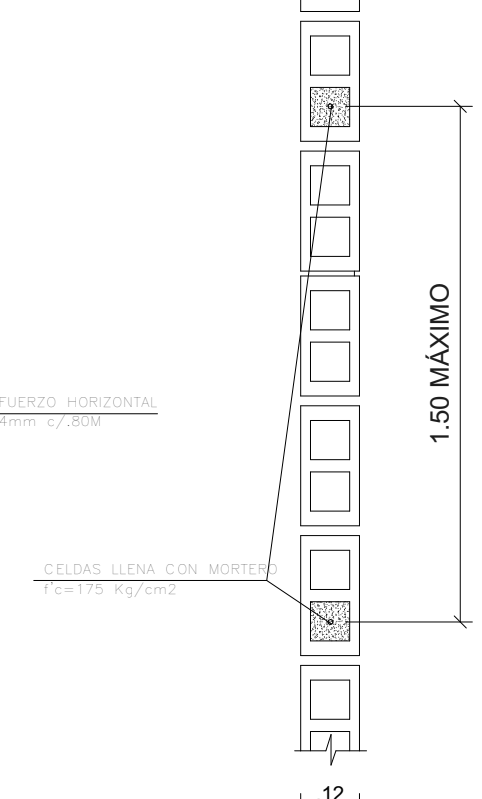


SECCIÓN C-C
ESC 1:12.5

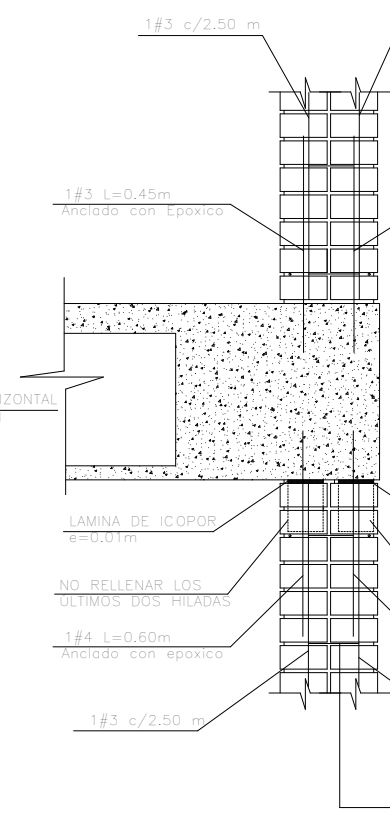


SECCIÓN B-B
ESC 1:12.5

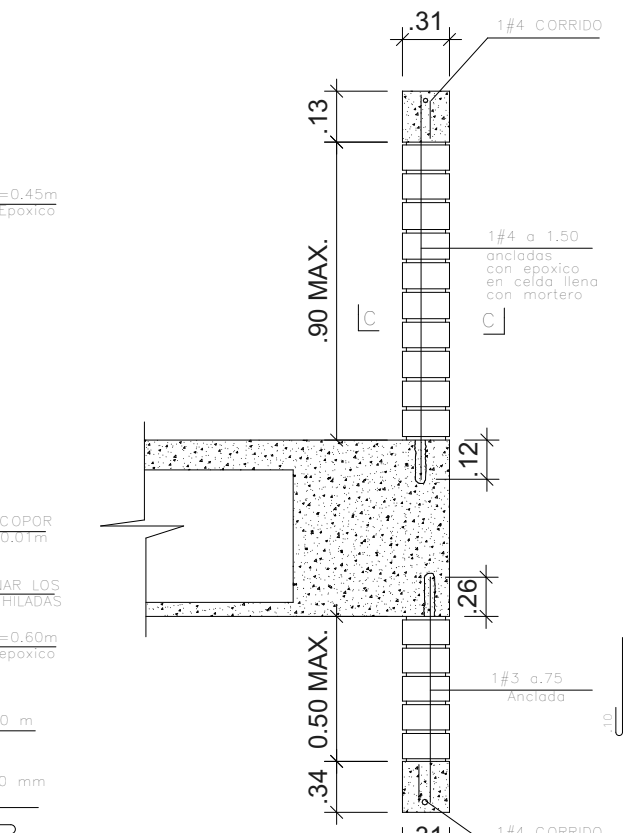

DETALLE DE DINTELES Y ANTEPECHOS
EN LADRILLO TOLETE
ESC 1:12.5

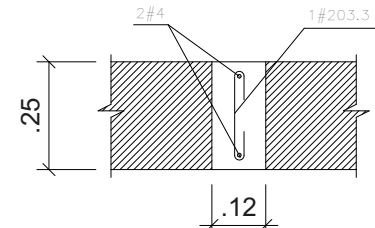


PARA MURO DOBLE
ESC 1:12.5

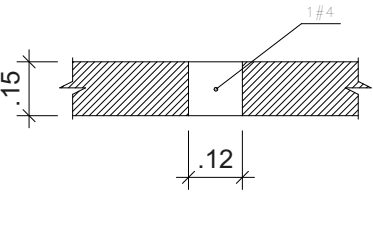

PARA MURO SENCILLO
ESC 1:12.5


NOTA IMPORTANTE: SECCIÓN D-D

LOS DISEÑOS DE ELEMENTOS ESTRUCTURALES DIFERENTES A LOS AQUÍ PRESENTADOS SERÁN RESPONSABILIDAD DE SUS FABRICANTES, CONSTRUCTORES O INSTALADORES, QUIENES DEBERÁN EJECUTARLOS DE ACUERDO CON LAS NSR-10, CON GRADO DE DESEMPEÑO BUENO

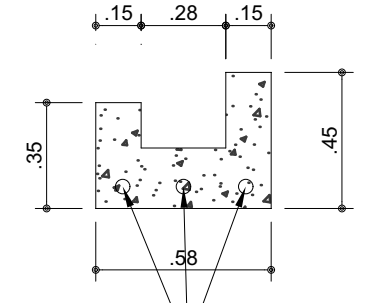


SECCIÓN VIGA CANAL
3#4

NOTA:
PARA EL ANCLAJE DE LAS BARRAS DE REFUERZO SE DEBE USAR UN ADHESIVO EPOXICO, TIPO HILTI O SIKA, O PRODUCTO DE RECONOCIDA CALIDAD.
SE DEBEN SEGUIR LAS RECOMENDACIONES DEL FABRICANTE.

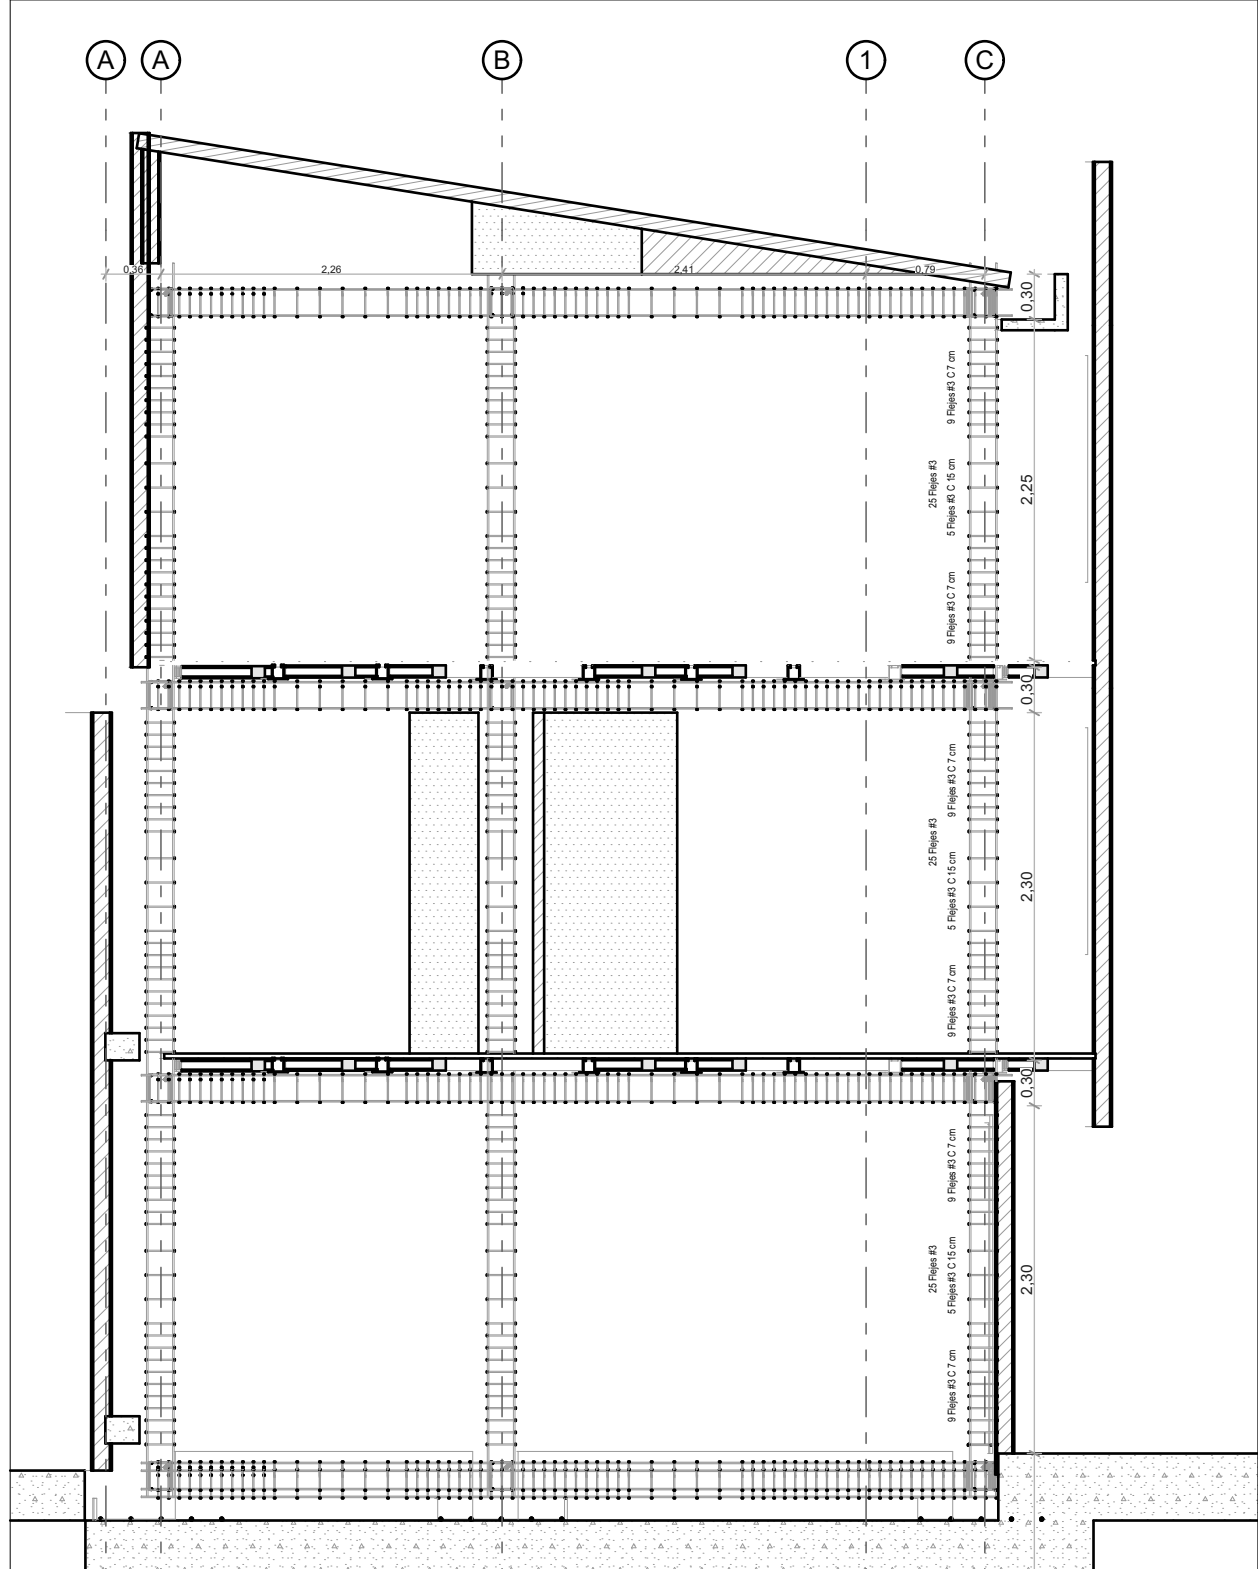

ALZADO LONGITUDINAL
Esc 1: 50

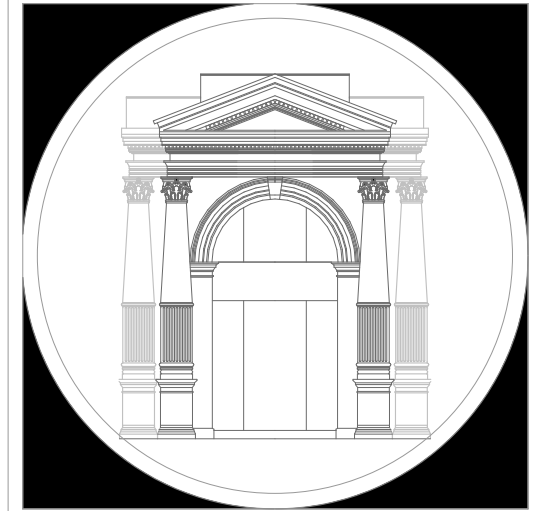

Unifamiliar
"San Esteban"

Localización:
Carrera 16 Calle 22

Arquitecto Proyectista:
Arturo Castro Pacheco
A311162015-1049634950
Arquitecto C.P.N.A.A.

Director de Construcción:

Titular
Nombre: Jeicot E. Rodriguez
Cédula: 6.774.038 de Tunja

Elementos no estructurales:
Nombre: _____
M.P.: _____

Contiene:
DETALLES NO ESTRUCTURALES
CORTE LONGITUDINAL

Digitó:
GRAPHICAD
C.C. 450 AÑOS
LOCAL 118 CRA 9-17-36

Escala:
Segun Indicación
ID:
E4/4
Fecha:
Abril de 2026