


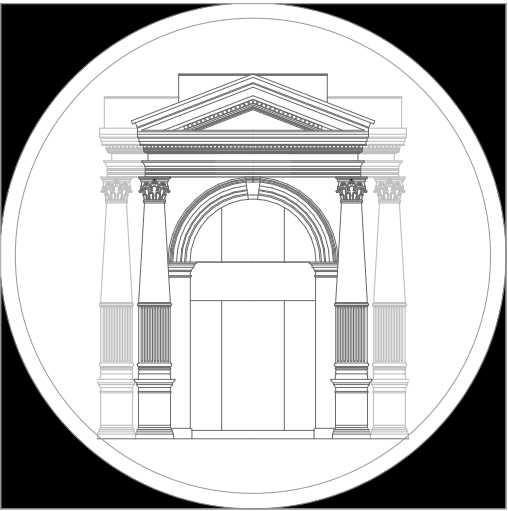

Unifamiliar
"San Esteban"

Localización:

Carrera 16 Calle 22

Arquitecto Proyectista:

Arturo Castro Pacheco
A311162015-1049634950
Arquitecto C.P.N.A.A.

Director de Construcción:

Titular

Nombre: Jeicot E. Rodriguez
Cédula: 6.774.038 de Tunja

Elementos no estructurales:

Nombre: _____
M.P.: _____

Contiene:

Digitó:


GRACIELA
C.C. 450 AÑOS
LOCAL 118 CRA 9-17-36

Escala:
Segun Indicación


Fecha:
09 de Marzo de 2026

ID:


HS

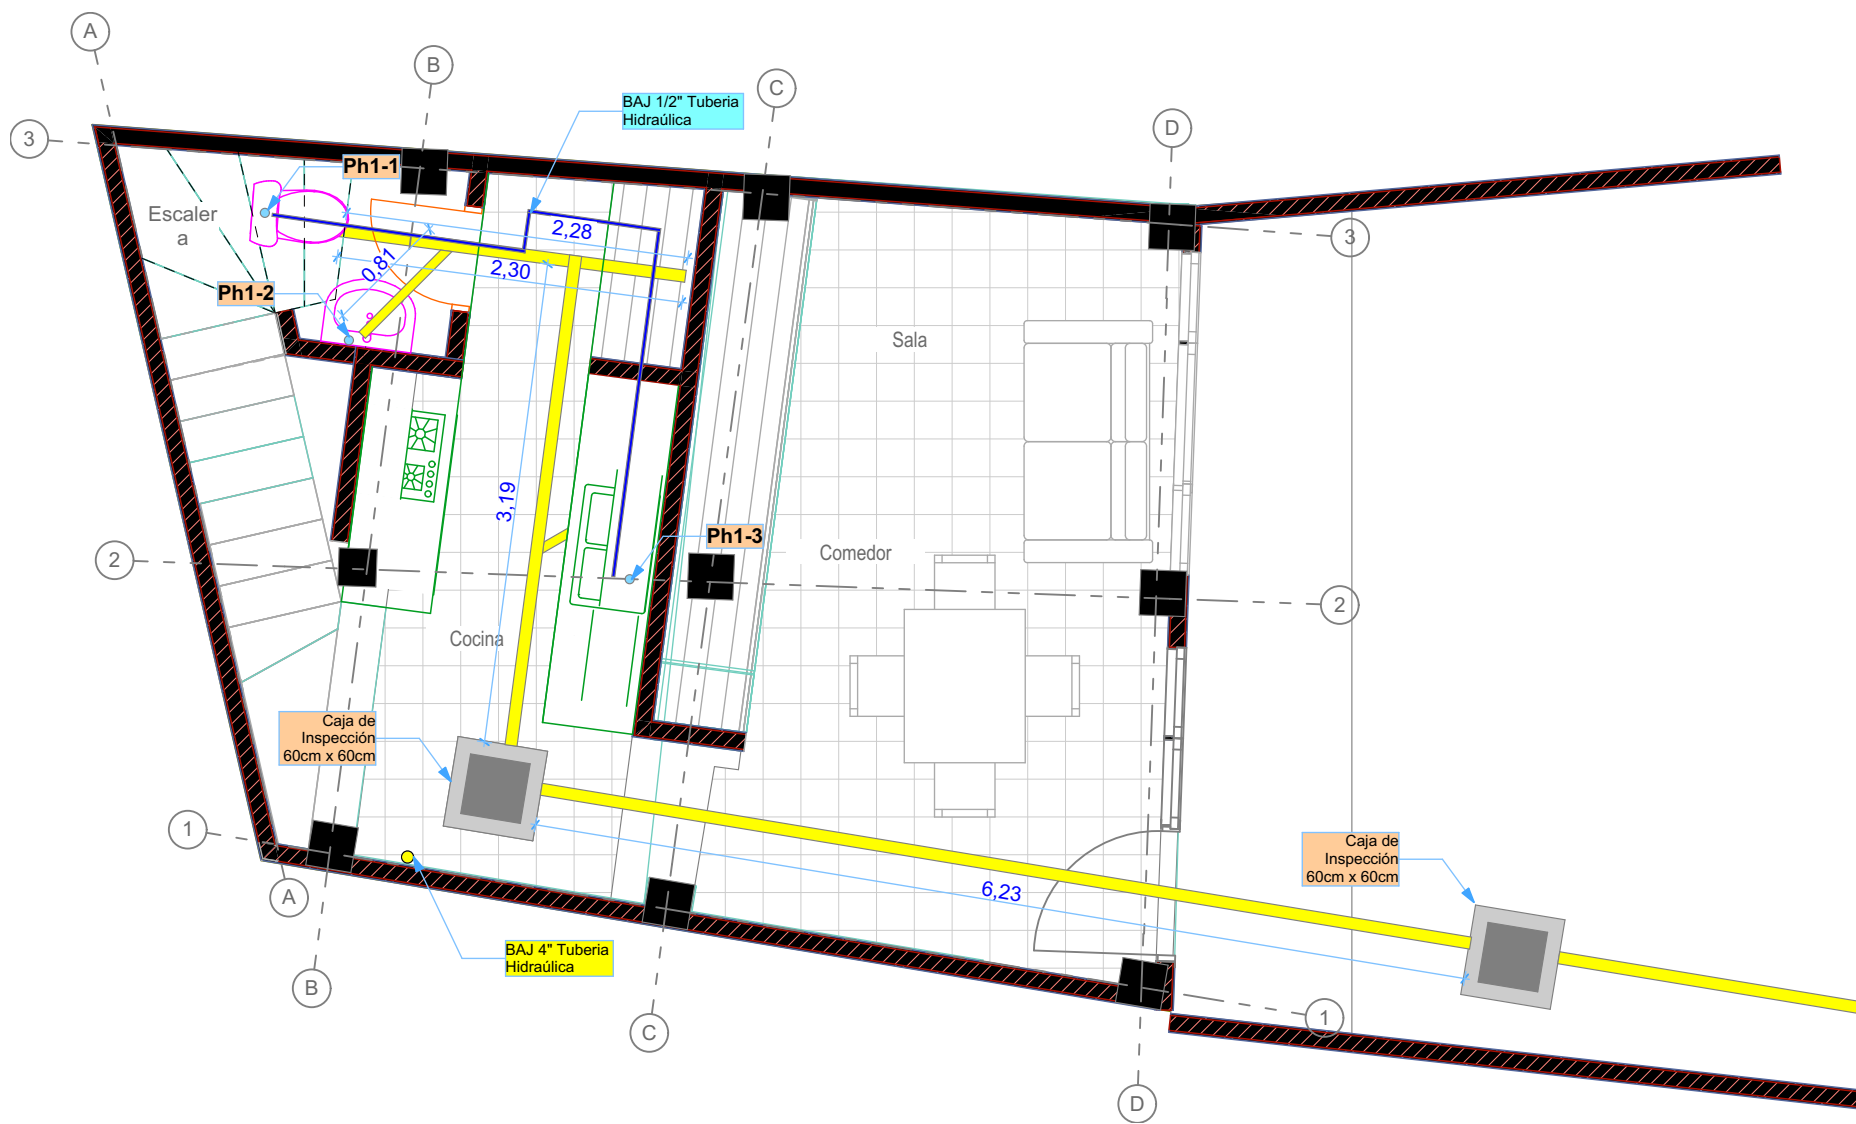


HIDROSANITARIO DE PRIMER PISO
ESC 1:50

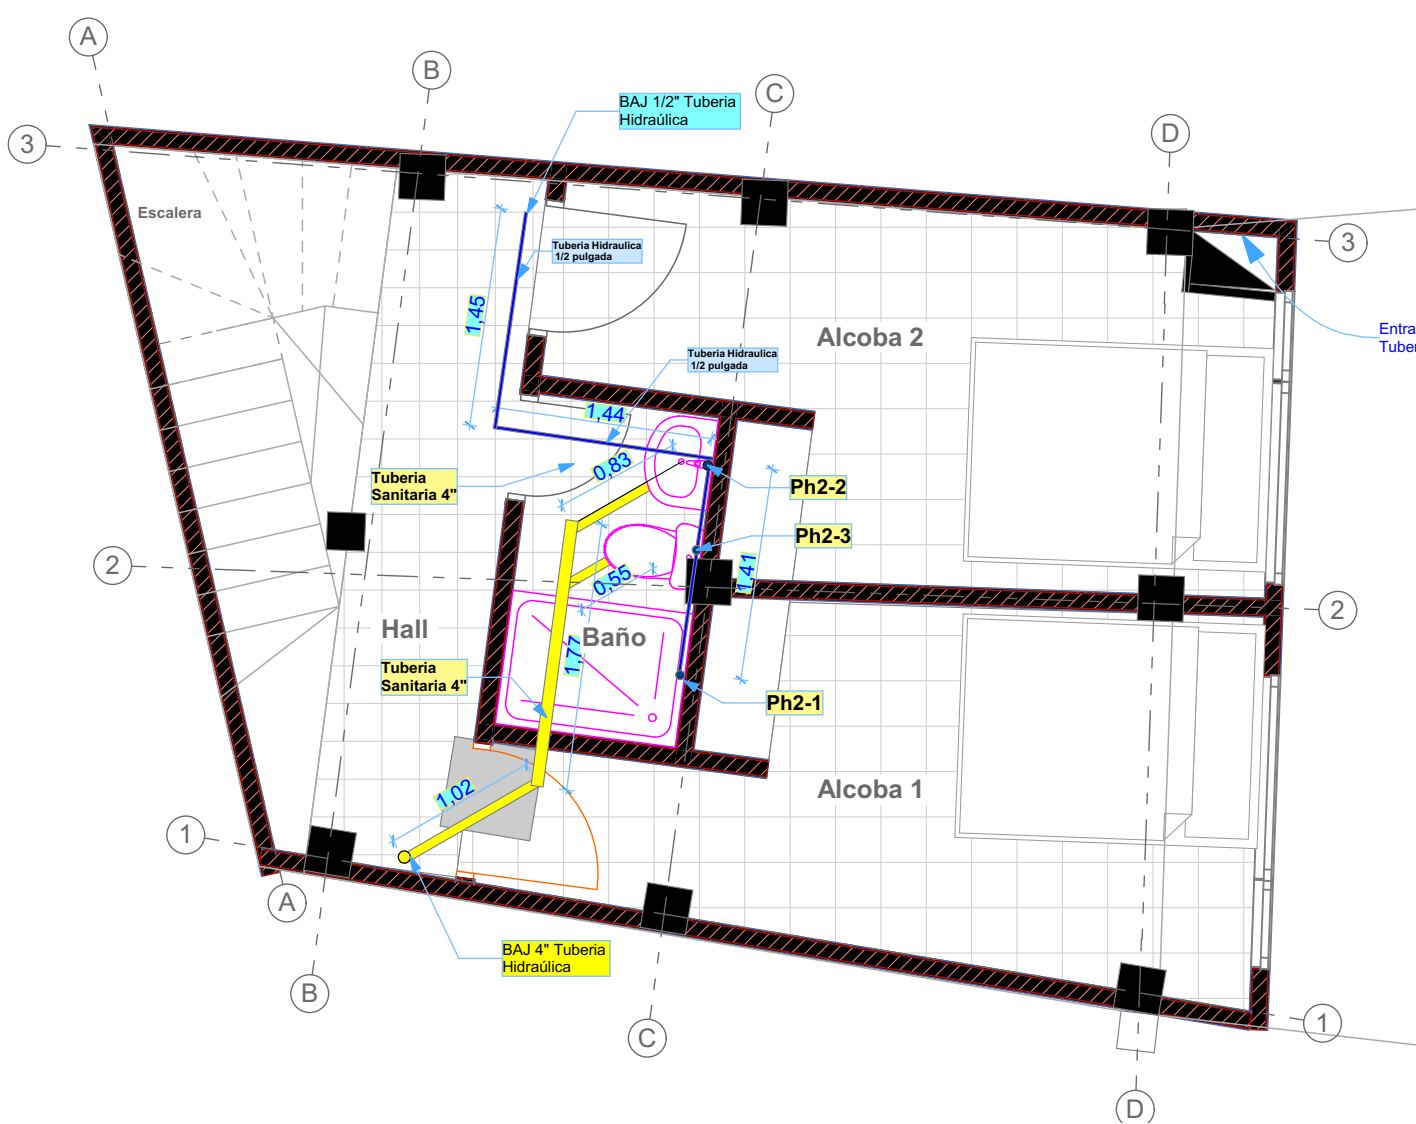

HIDROSANITARIO DE SEGUNDO PISO
ESC 1:50

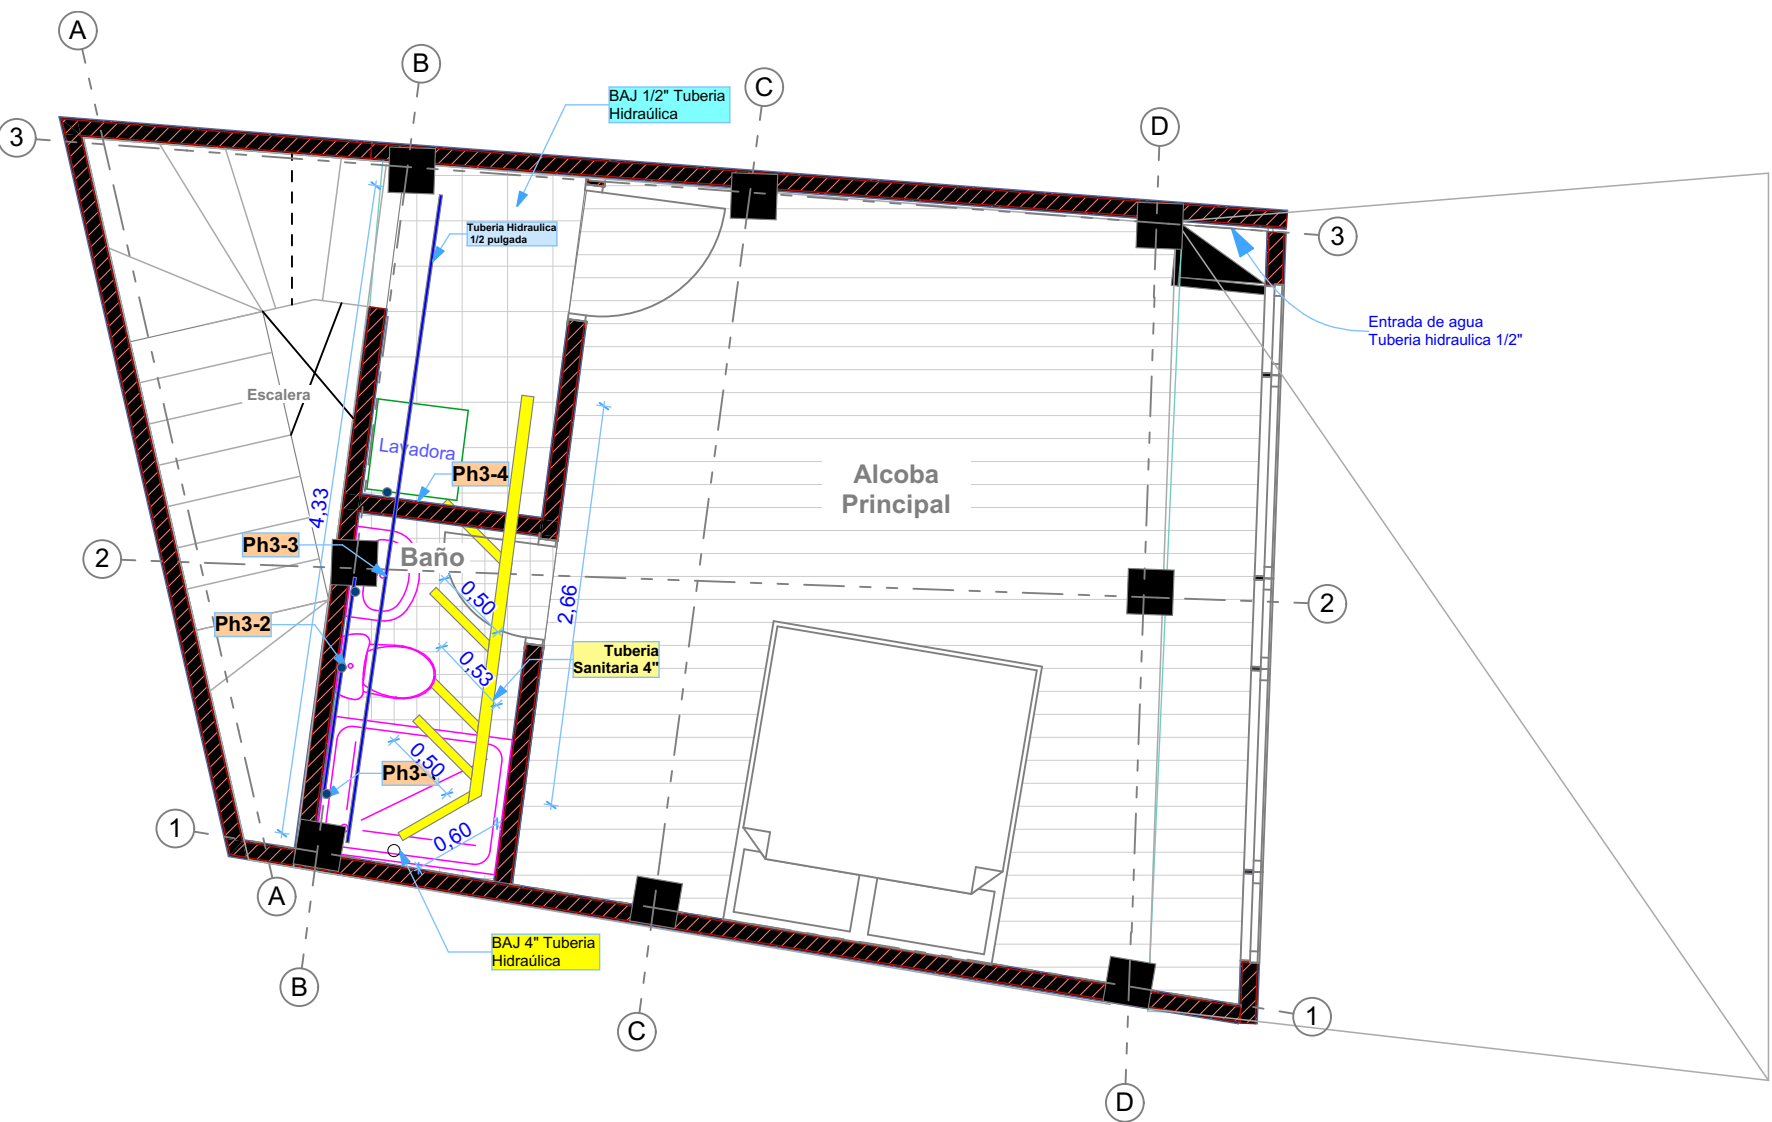

HIDROSANITARIO DE TERCER PISO
ESC 1:50

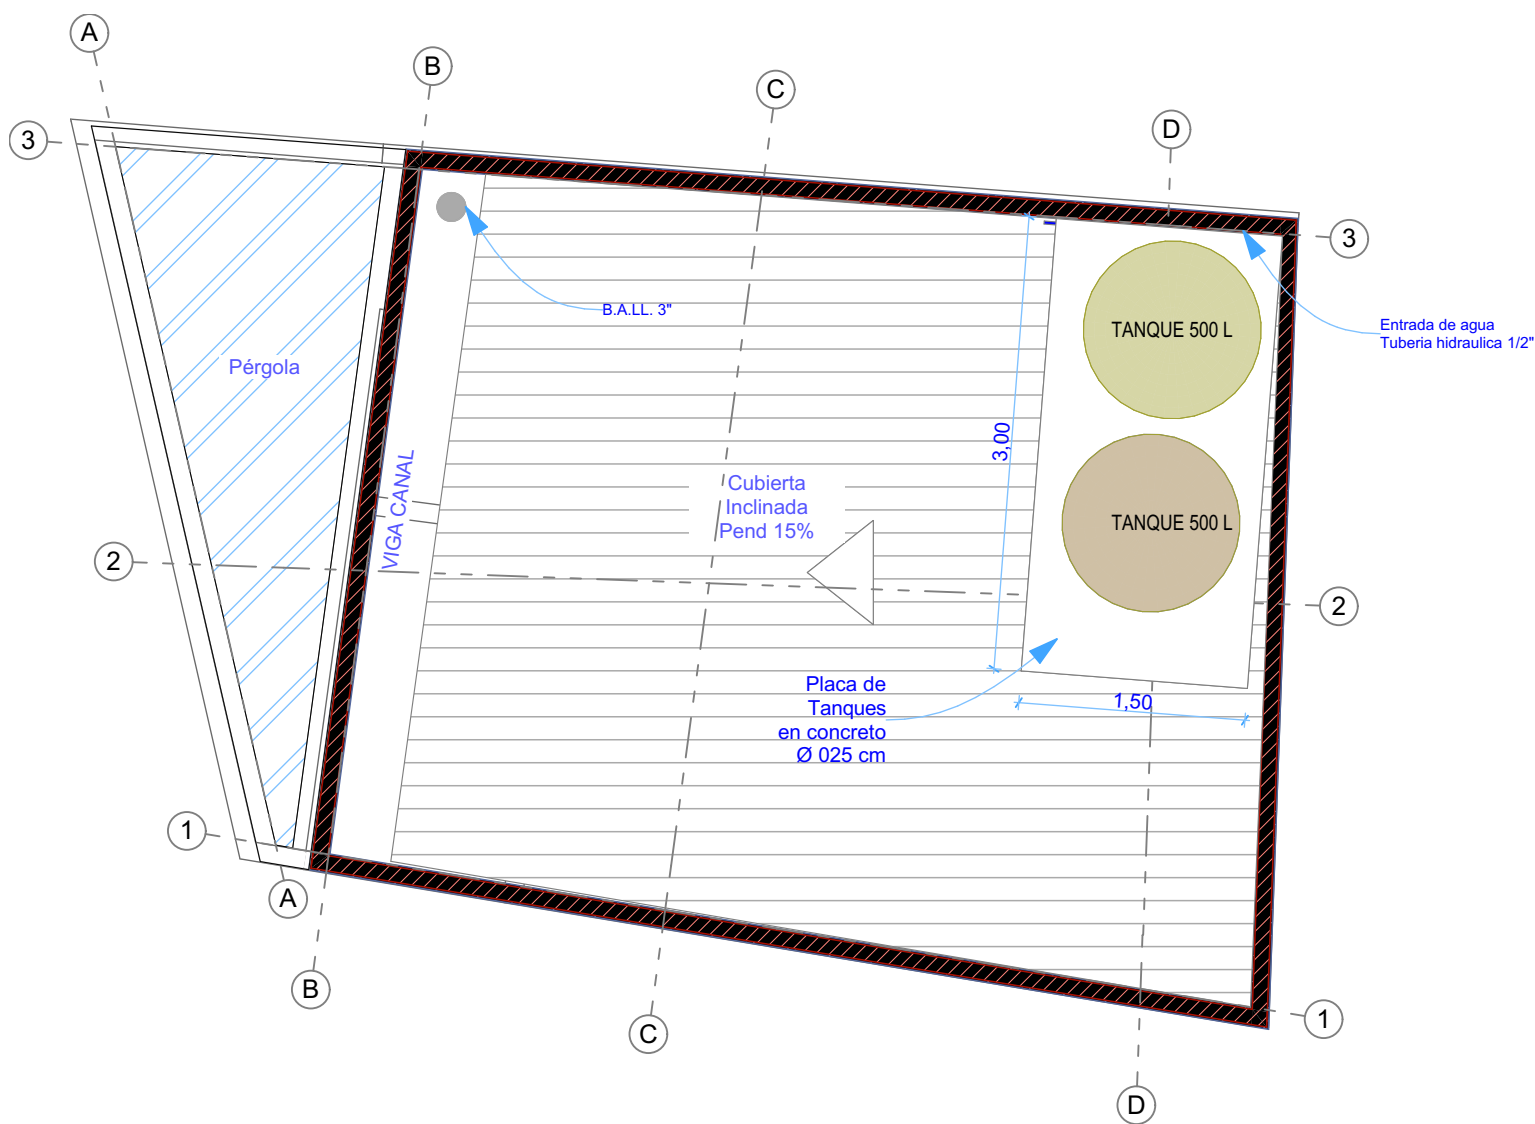

HIDROSANITARIO DE CUBIERTAS
ESC 1:50